

C.F.F.

1^{er} arrondissement.

Ligne: Lausanne - Bienne.

Double voie Ependes - Yverdon.
avec déviation de la ligne à partir du

Km. 35.648⁵⁰ (Valentin)

Commune de Gressy.
Commune d'Yverdon.

Plan de situation.

Echelle 1:1000.

R.P.N. 373.60

Reçu de M^r Pallaton comme
plan explicatif de la convention
N^o 11078, du 24 janvier 1934,
le 11 mars 1934.


LE SECRÉTAIRE PRÉPOSÉ AU REGISTRE FONCIER

Arrel.

Lausanne, le août 1929

Fellera



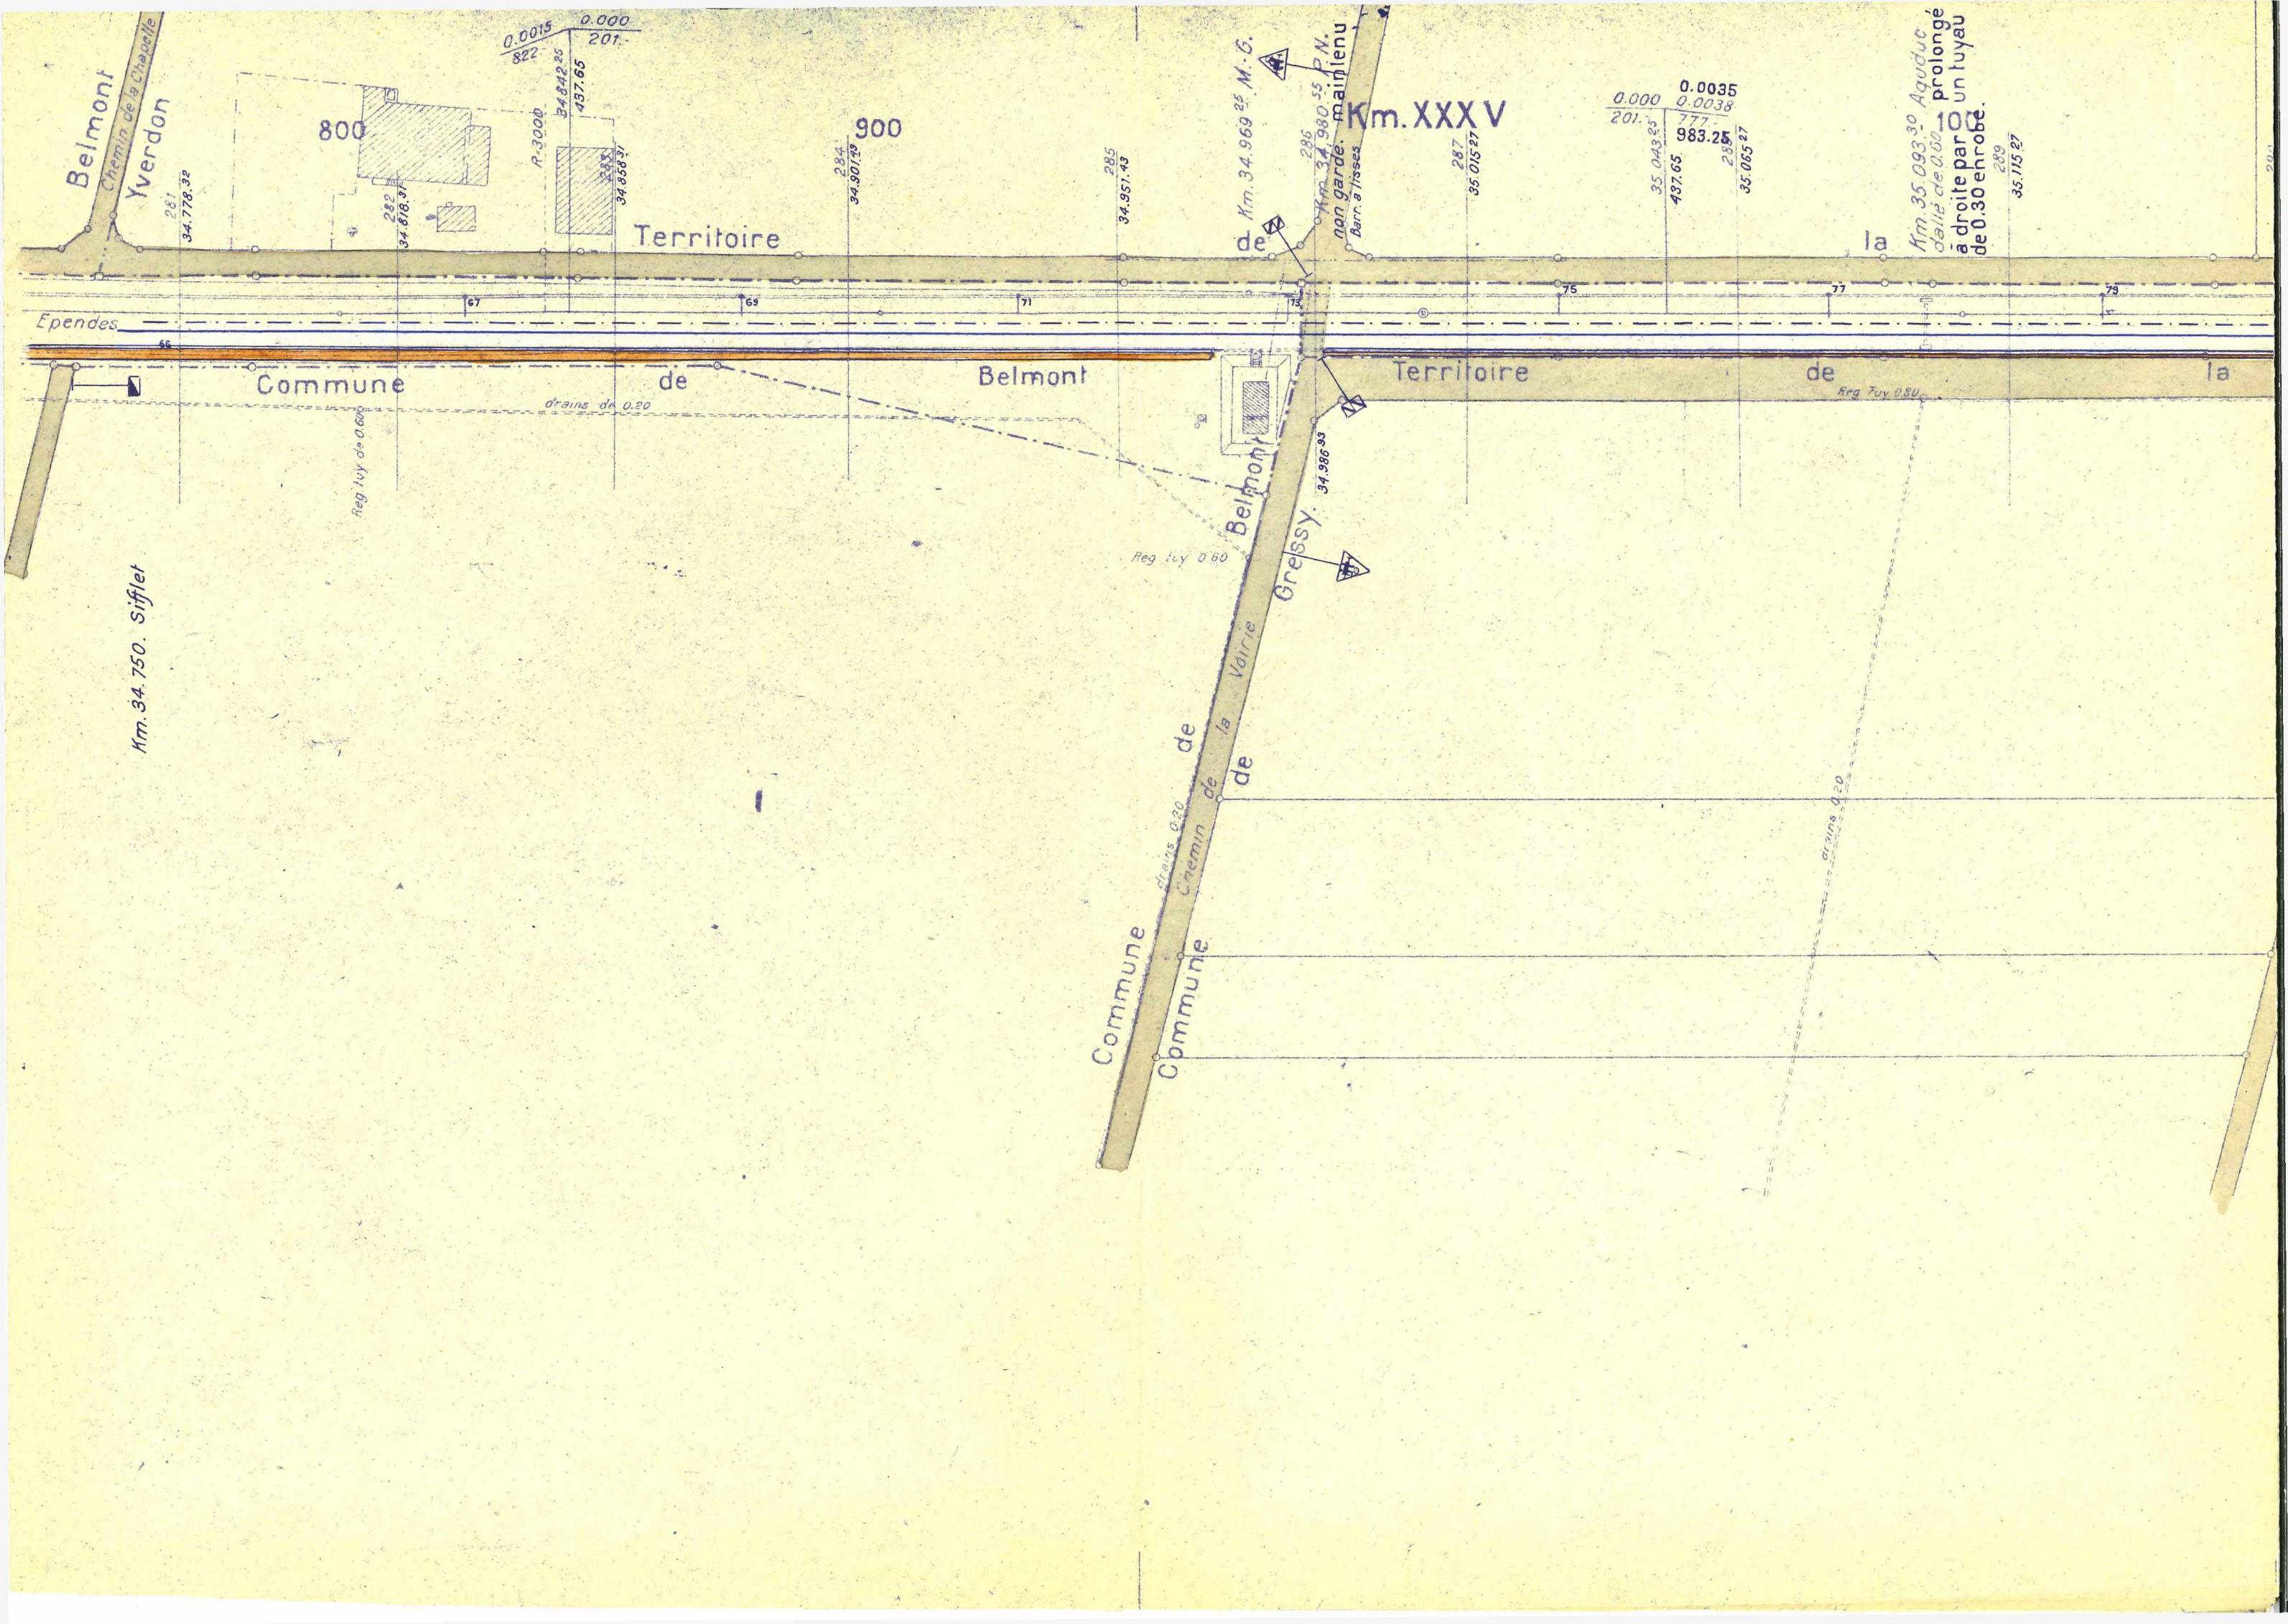

35.165 27

200

commune

291
35.215 27

Km. 35.250. Sifflet

292
35.265 27

300

293
35.312 69

294
35.362 69

d'Yverdon.

400

295
35.412 86

296
35.462 86

500

297
35.512 86

298
35.562 86

commune

de

Gressy

Km. 35 350. Signal p^r le mecanicien.
Ordre de siffler.

Commune

Commune

de

Gressy

d'Yverdon.

600

700

800

900

Km. XX

501

501

Km. 35.95575 Ag. de 1.80
R.7 (434.549)

x 433.57

Km.

R.8 (434.177)

P.N. avec b. à b. manœuvrées à distance maintenues non gardées. B. à b. rem. places par des barrières à lisse.

Km. 35.64850 Origine de la déviation
R. 600

Km. 35.819.00 Tuyaux en ciment de 0.35 enrobés de béton

Km. 35.941.00 Tuyaux en ciment de 0.20 enrobés de béton.

Km. 35.974.00 P.N. public non gardé de 4m de large
Barrières à lisses

Km. 36.00150 Tuyaux en ciment de 0.50 enrobés de béton.

En Gravel

Cul de sac de travaux.

Tuyaux 0.35

Drains 10

Drains 0.10

Pente 10.50

Palier

Palier

Palier

Palier

Palier

Palier

Palier