

Str. Palen

431.21. Arrivée tuyau 0.30. Ecoulement eaux du P.I.

Km. 36.085. Tuy. cim. de 0.20. Enrobement en béton.

Km. 36.152 Tuyaux en ciment de 0.25 enrobés de béton

36.0

0.0035
983.25

0.010
525.22

36.026 59
434.22

36.028 50

36.048 50

36.068 50

36.088 50

36.108 50

36.128 50

36.148 50

36.168 50

36.188 50

2.
Regard
36.208 50

36.228 50

36.248 50

36.262 22

36.282 22

36.302 22

36.322 22

36.342 22

36.362 22

Chemin public

Drains 12°/m

Tuy. 0.25

Km. 36.230. Signal p^r le mécanicien
Ordre de siffler

Drains 12°/m


Ecoulement des eaux du P.I. Tuyau de 0.30

R. 10 (434.350)

R. 9. (434.158)

R = 600

Chemin de fer

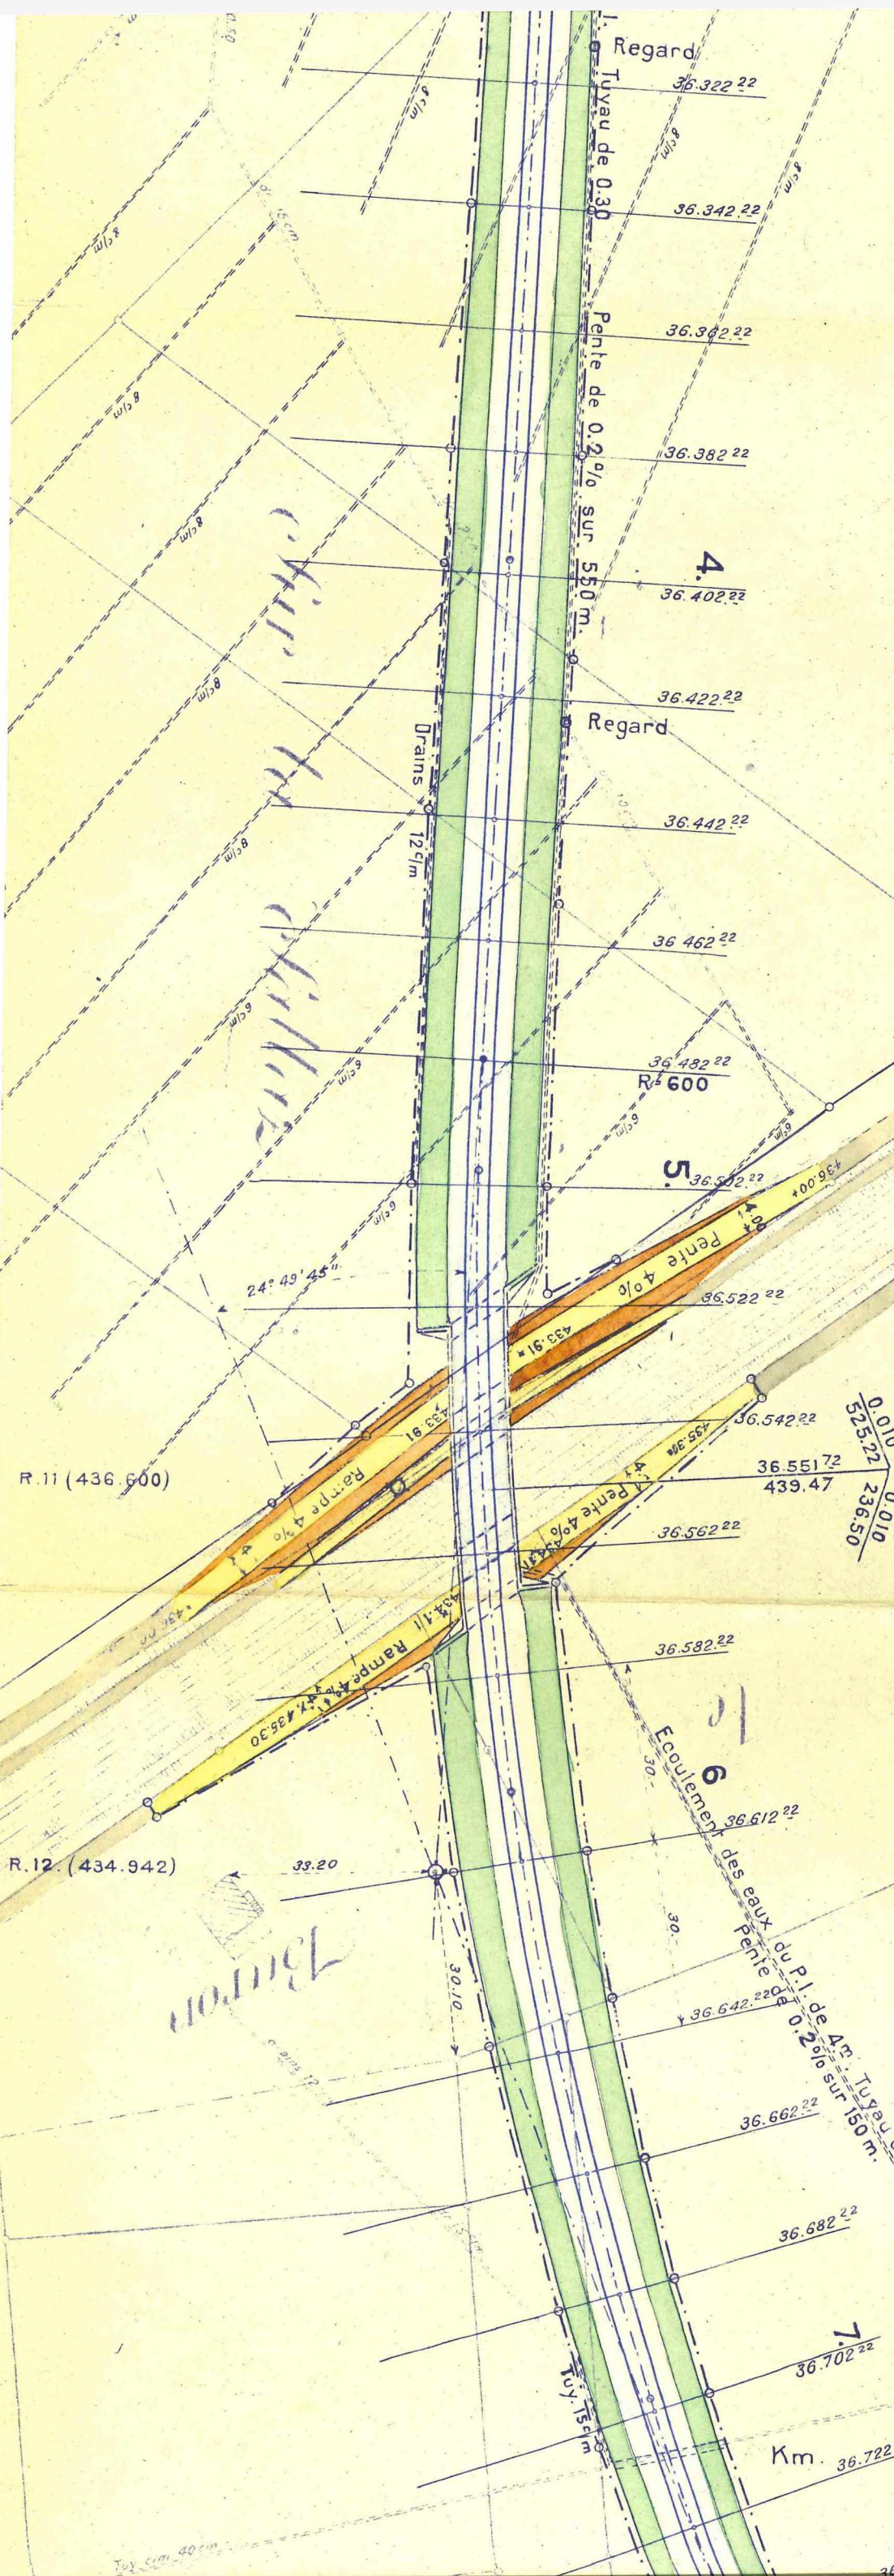

Viaduc du Buron

- Km. 36.531.⁰² P.I. pour route cantonale de 10^m d'ouv. droite et 4^m 20 de haut. libre.
- Km. 36.542.³⁷ Sentier p^r piétons de 2^m00 de larg. et 2^m20 de h.l.
- Km. 36.551.⁷² Pont sur le Buron de 8^m 50 d'ouv. droite.
- Km. 36.566.⁹² P.I. pour chemin latéral de 4^m d'ouv. droite et 4^m00 de haut. libre.

Km. 36.722.²² 36.709.- Tuy. cim. 0.40 Enrobement de béton.