


Annexe 5 : plan de situation du 14.03.2019



- ### Légende
-  Existant
 -  Nouveau
 -  À démolir
 -  Lignes de sécurité tactilo-visuelles, largeur 30cm.
 -  Champ d'éveil, largeur 60cm.
 -  Chemins / Quai nouveaux
 -  Abri à vélos nouveau
 -  Abri à vélos existant
 -  Marquise nouvelle
 -  Marquise à démolir
 -  Couverts nouveaux
 -  Passerelles à signaux nouvelles
 -  Passerelles à signaux à démolir
 -  Jouis supports existants
 -  Jouis supports nouveaux
 -  Jouis supports à démolir
 -  Jouis d'amarrages existants
 -  Jouis d'amarrages nouveaux
 -  Jouis d'amarrages à démolir
 -  Rampes nouvelles
 -  Candélabres nouveaux

N° voies	V _n	V _f	V _a
901	-	95km/h	90km/h
902	145km/h	130km/h	120km/h
903	145km/h	130km/h	120km/h
904	145km/h	130km/h	120km/h