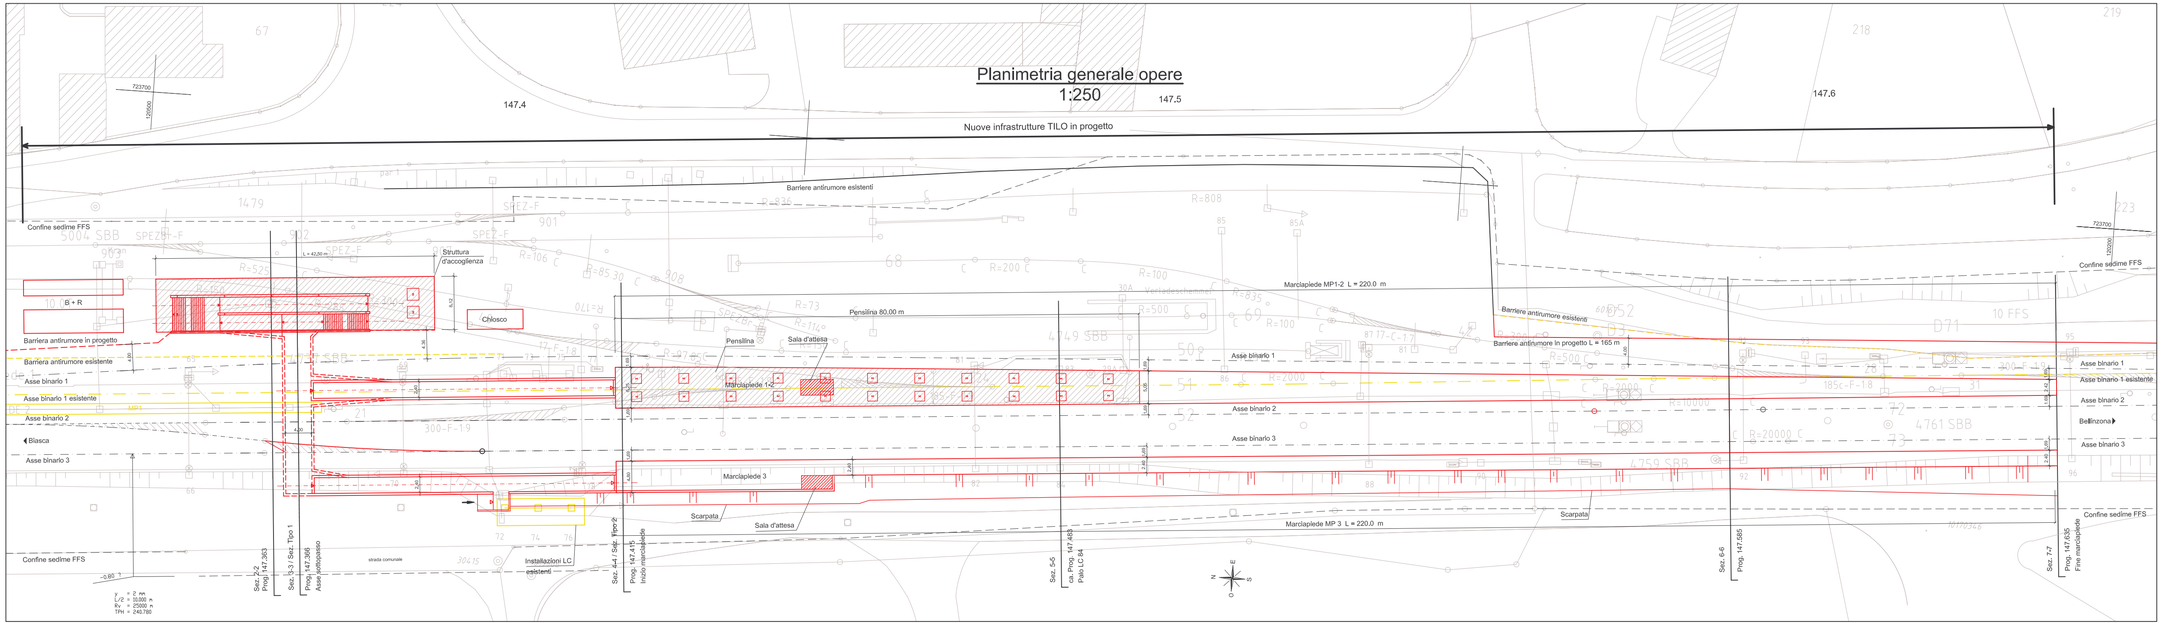

RIFERIMENTI:

- Dis. TI00377 - 2: Sottopasso - situazione e sezioni
- Dis. TI00377 - 3: Sezioni correnti
- Dis. TI00377 - 4: Sezioni tipo
- Dis. TI00377 - 5: Plano installazioni di cantiere
- Dis. TI00377 - 6: Plano di picchettaggio

DATI LINEA FERROVIARIA:

- V_{fmax} : 125 km/h

LEGENDA:

Esistente
Nuovo
Da demolire

SCALE GRAFICHE:

0 2.5 5.0 7.5 10.0 12.5 1:250

CSD Ingegneri SA
Via Lucchini 12, CH 6901 Lugano
Tel. +41 091 921 07 26
Fax +41 091 921 07 29
E-mail lugano@csd.ch
www.csd.ch

N° Dis. CSD	TI000377-1
Formato	1572x450
Disegnato	LSO
Controllato/Approvato	LSO - 13.03.2007

Castione-Arbedo — Km 146.900 - 147.900

TILO
Ristrutturazione Stazione
Castione-Arbedo

Scala	1:250
Nr. Plano	-
File	-
Linea	600

Planimetria opere civili — Progetto di pubblicazione

SBB
Projekt-Management
Zentralstrasse 1
6002 Luzern

SBB CFF FFS