




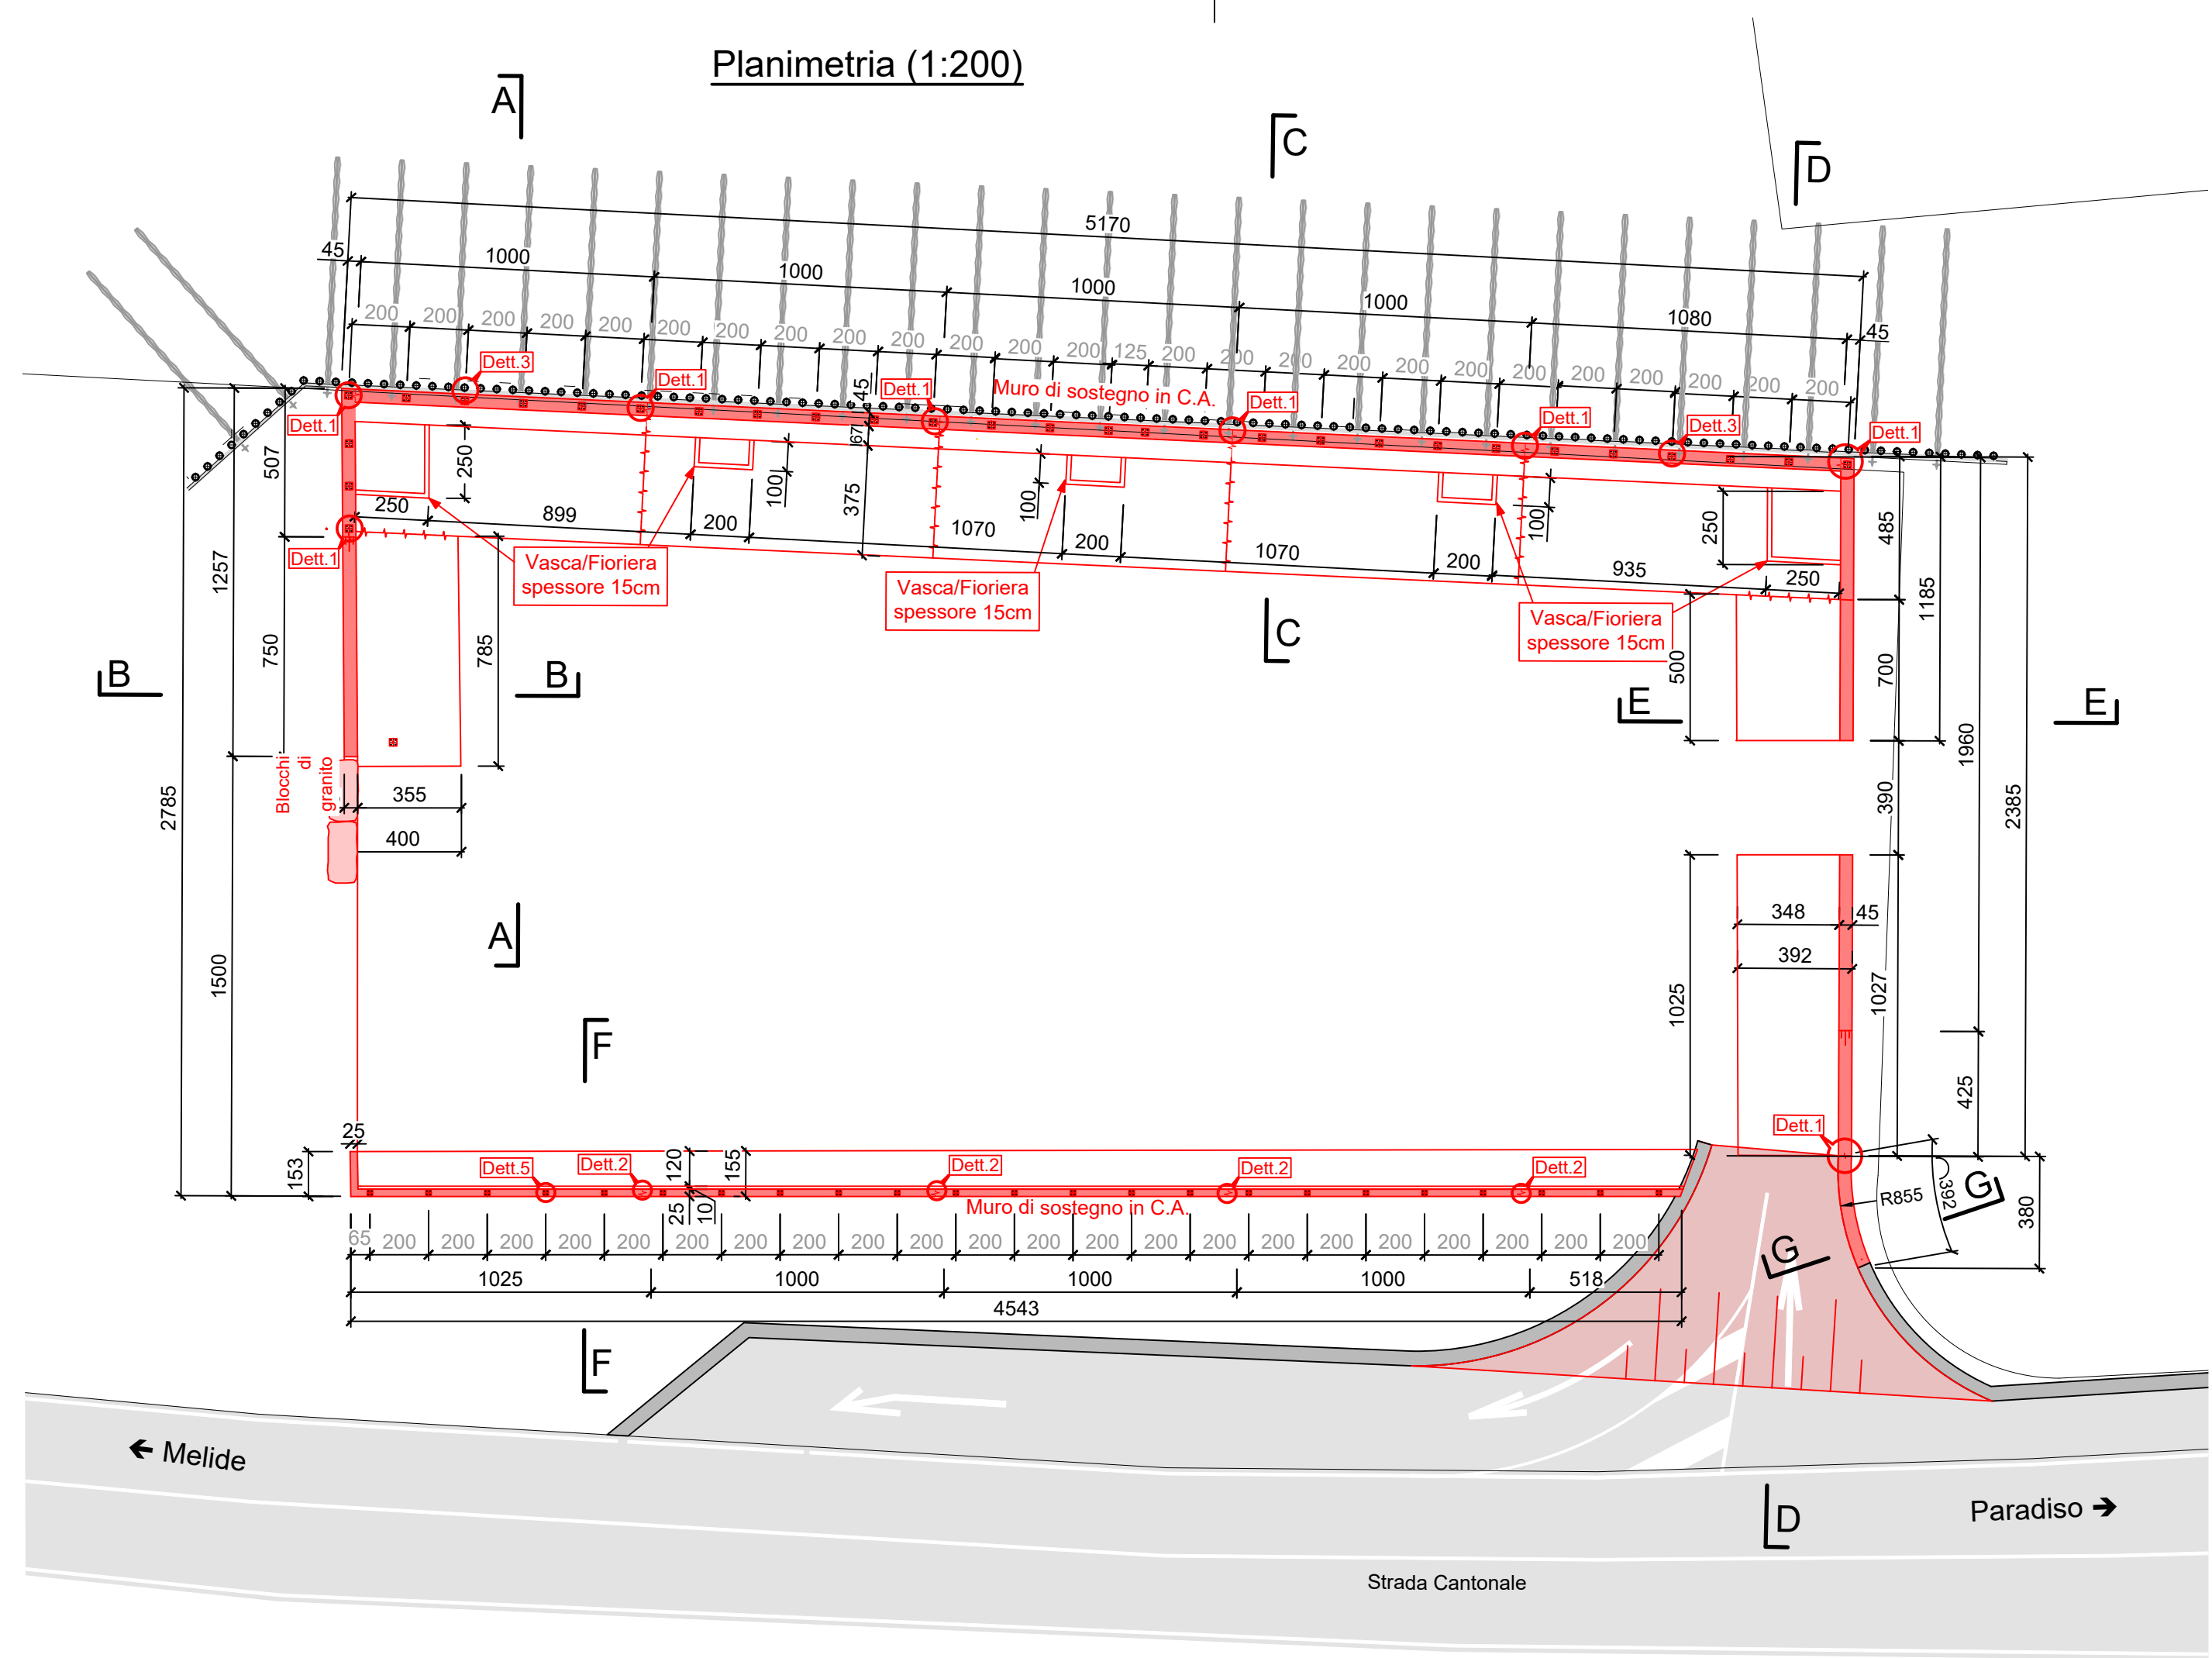


Pianta fondazione muretto in curva (1:50)

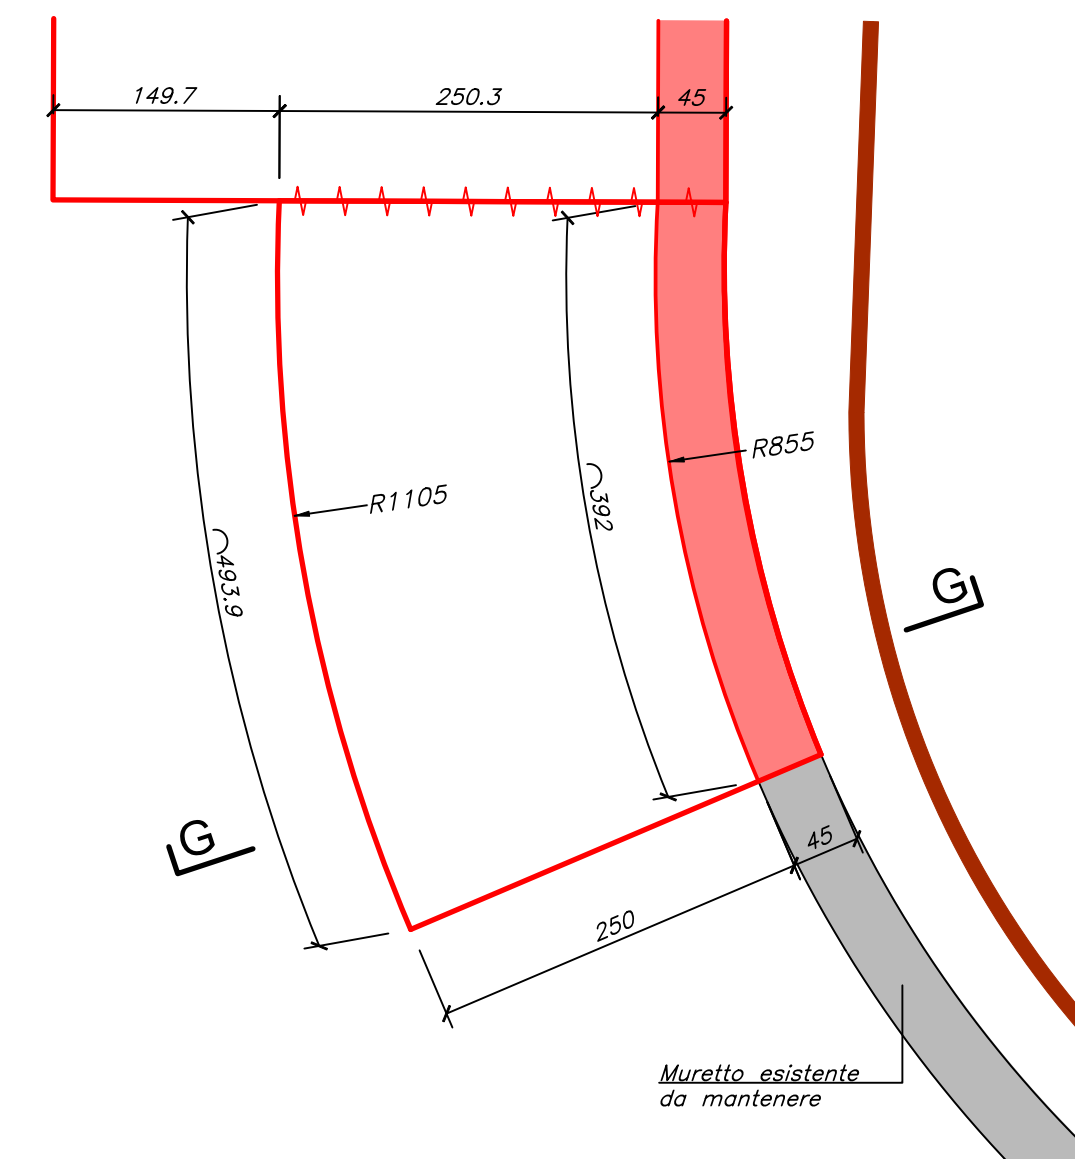


Sezione A-A (1:100)

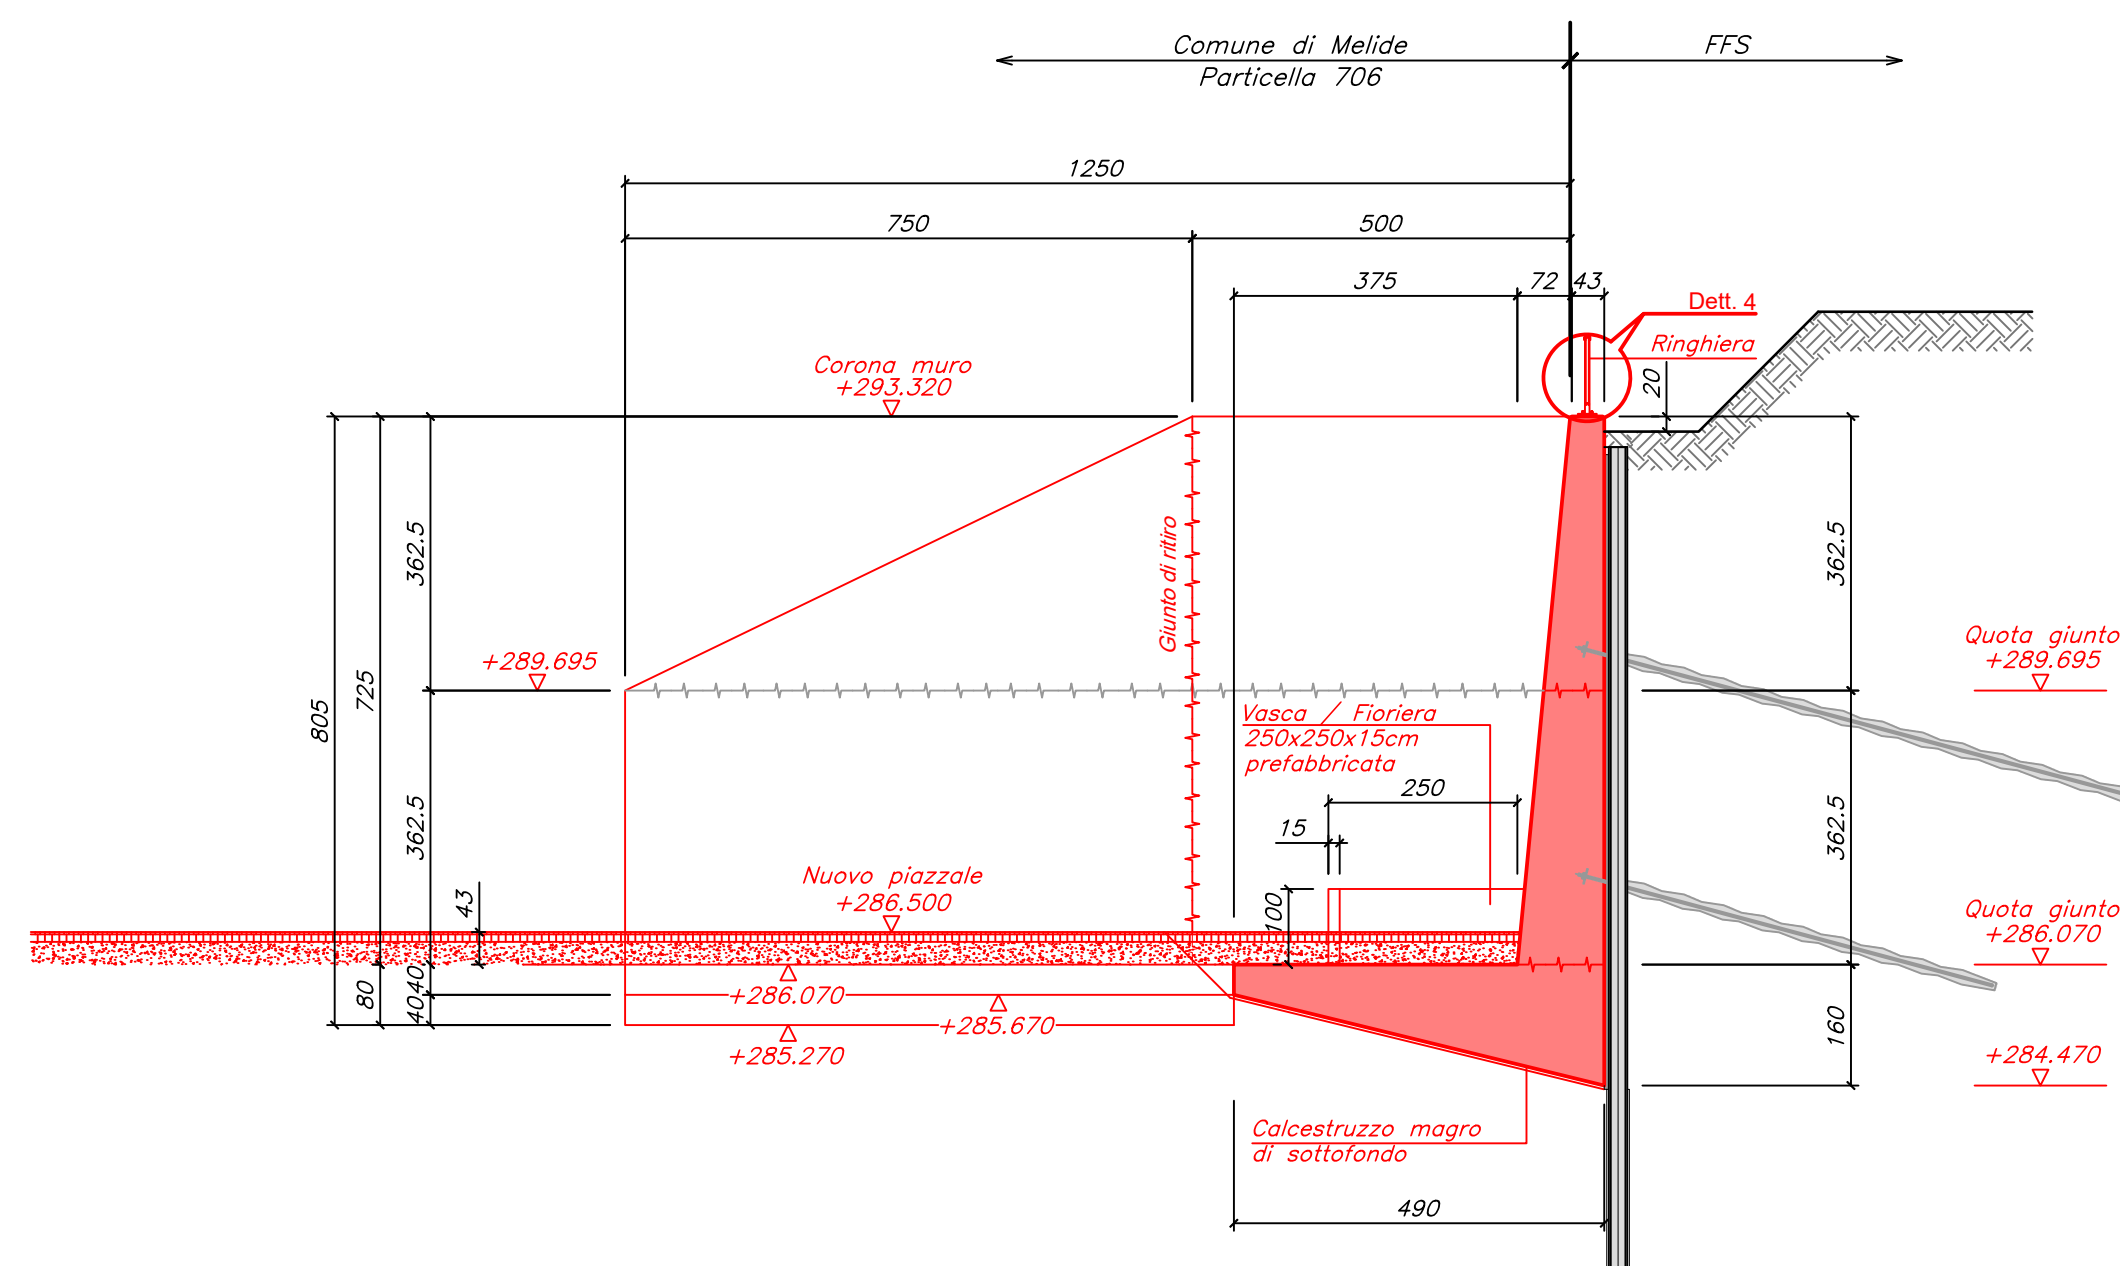


Sezione B-B (1:100)

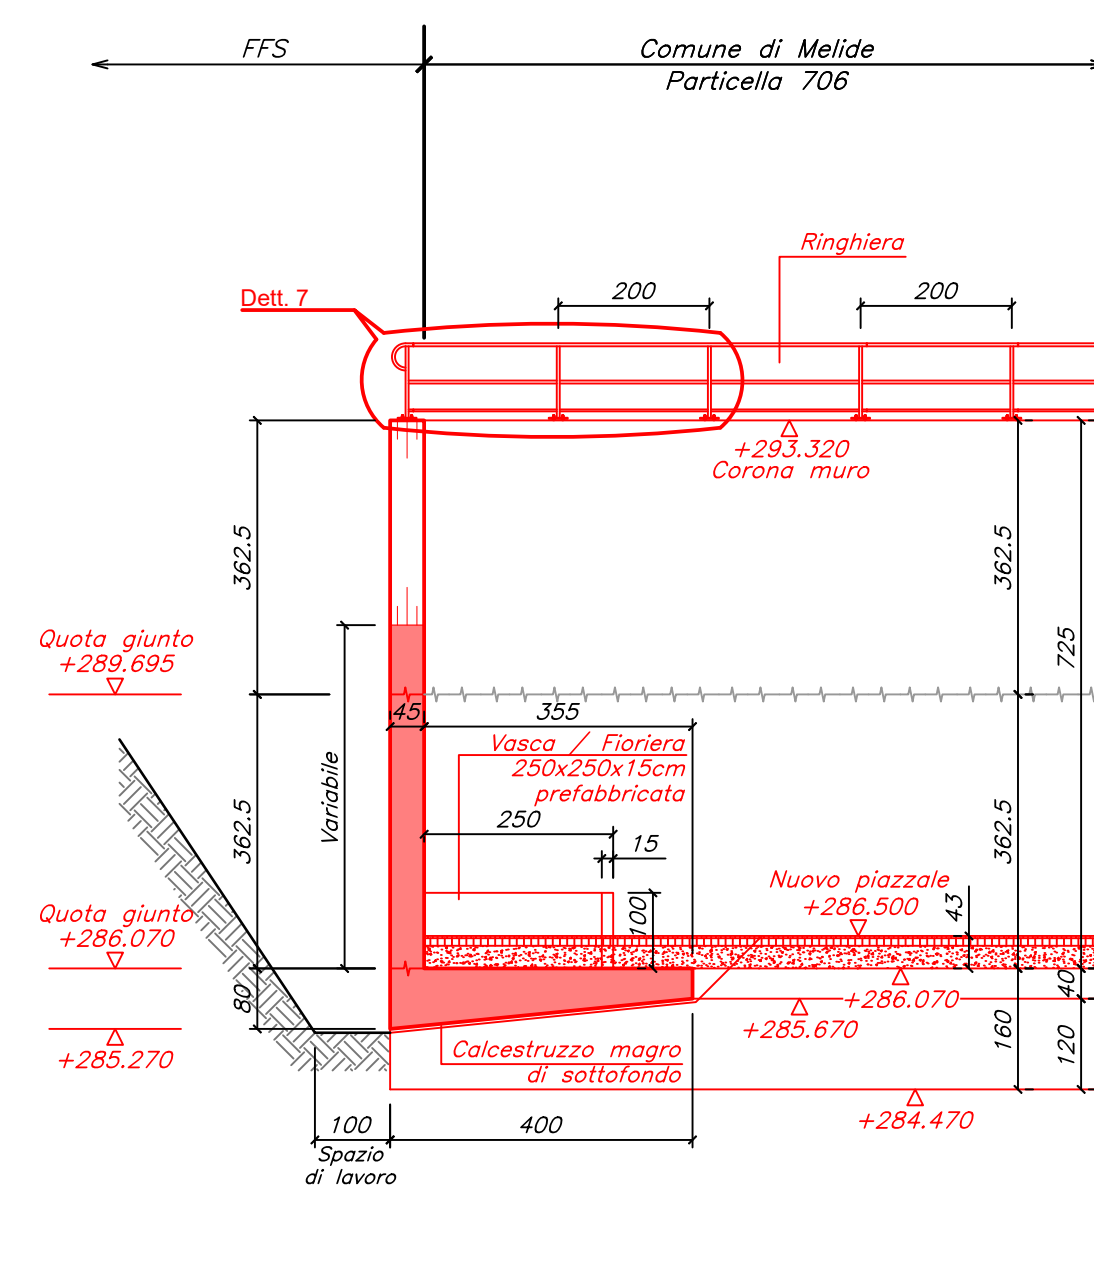


Dettaglio 5 (1:10)

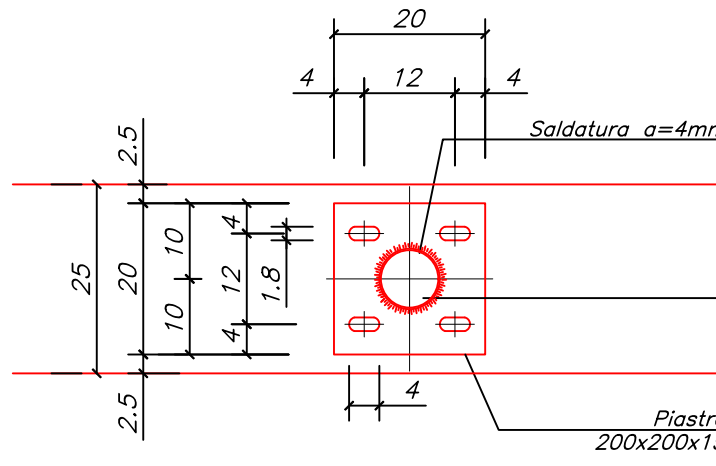


Dettaglio 6 (1:10)

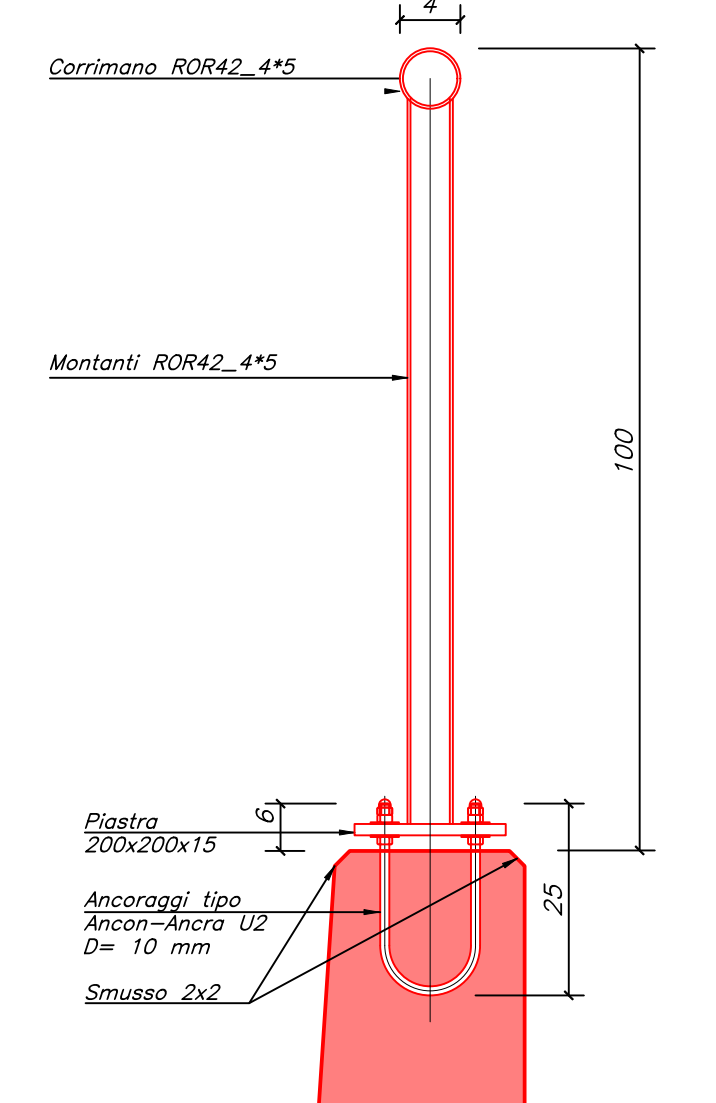


Sezione C-C (1:100)

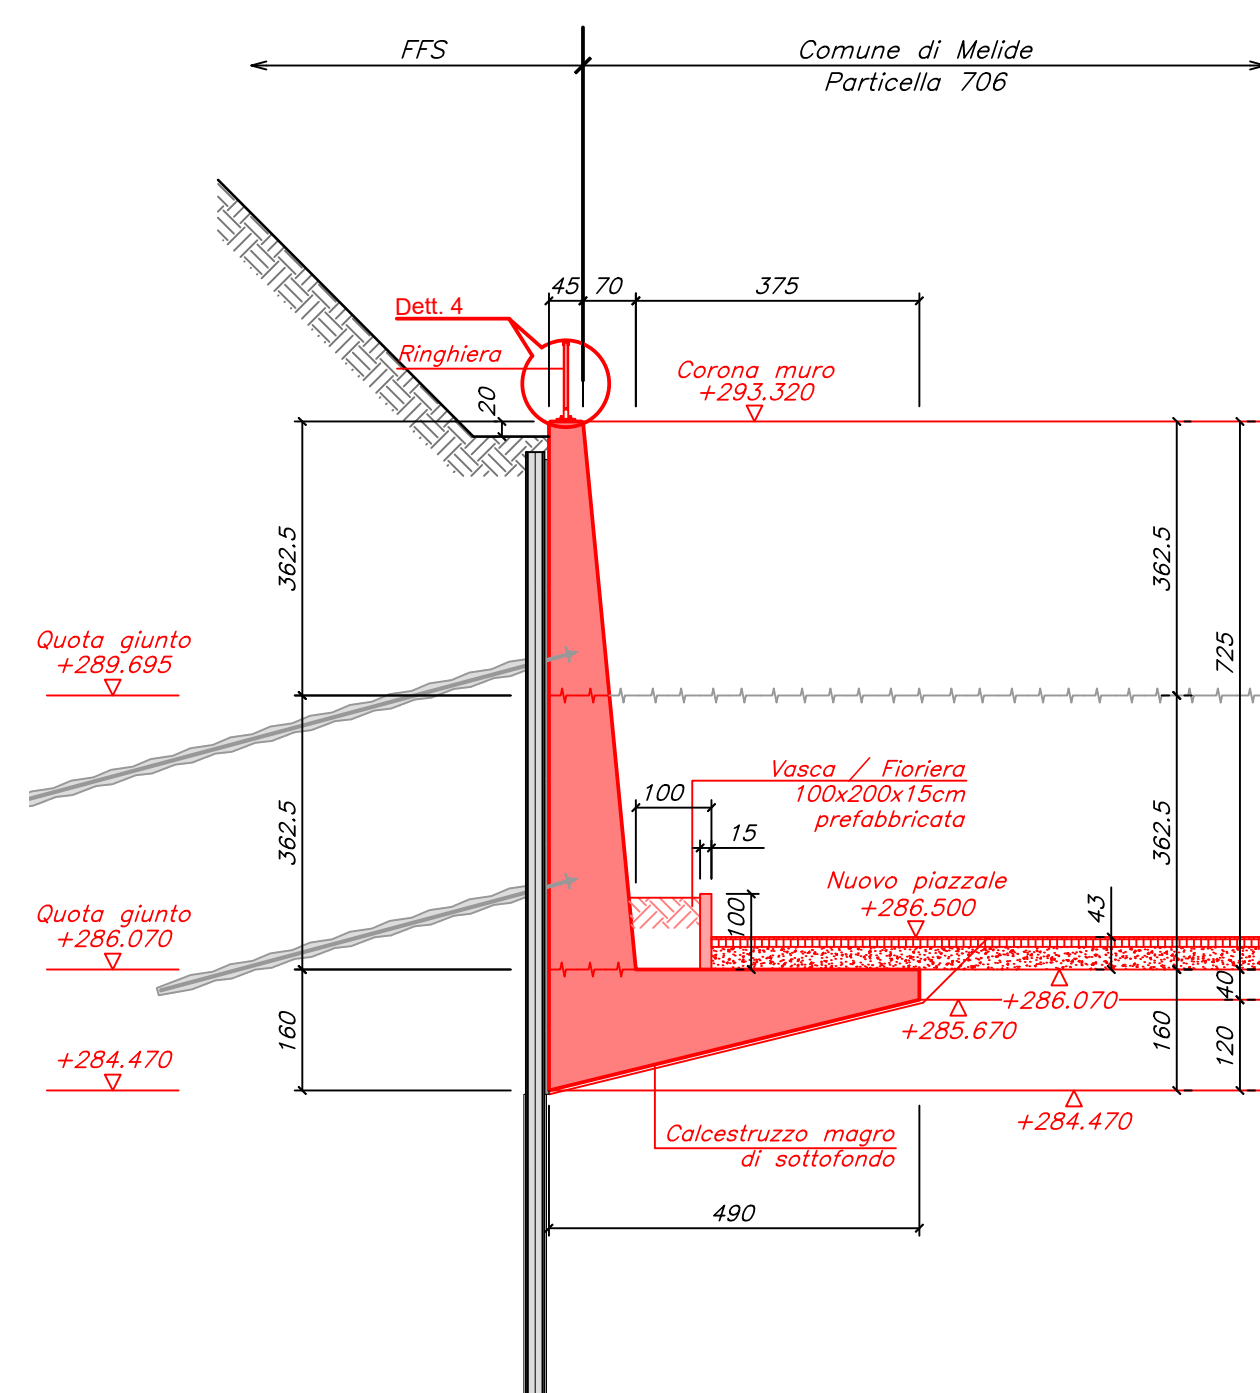


Sezione E-E (1:100)

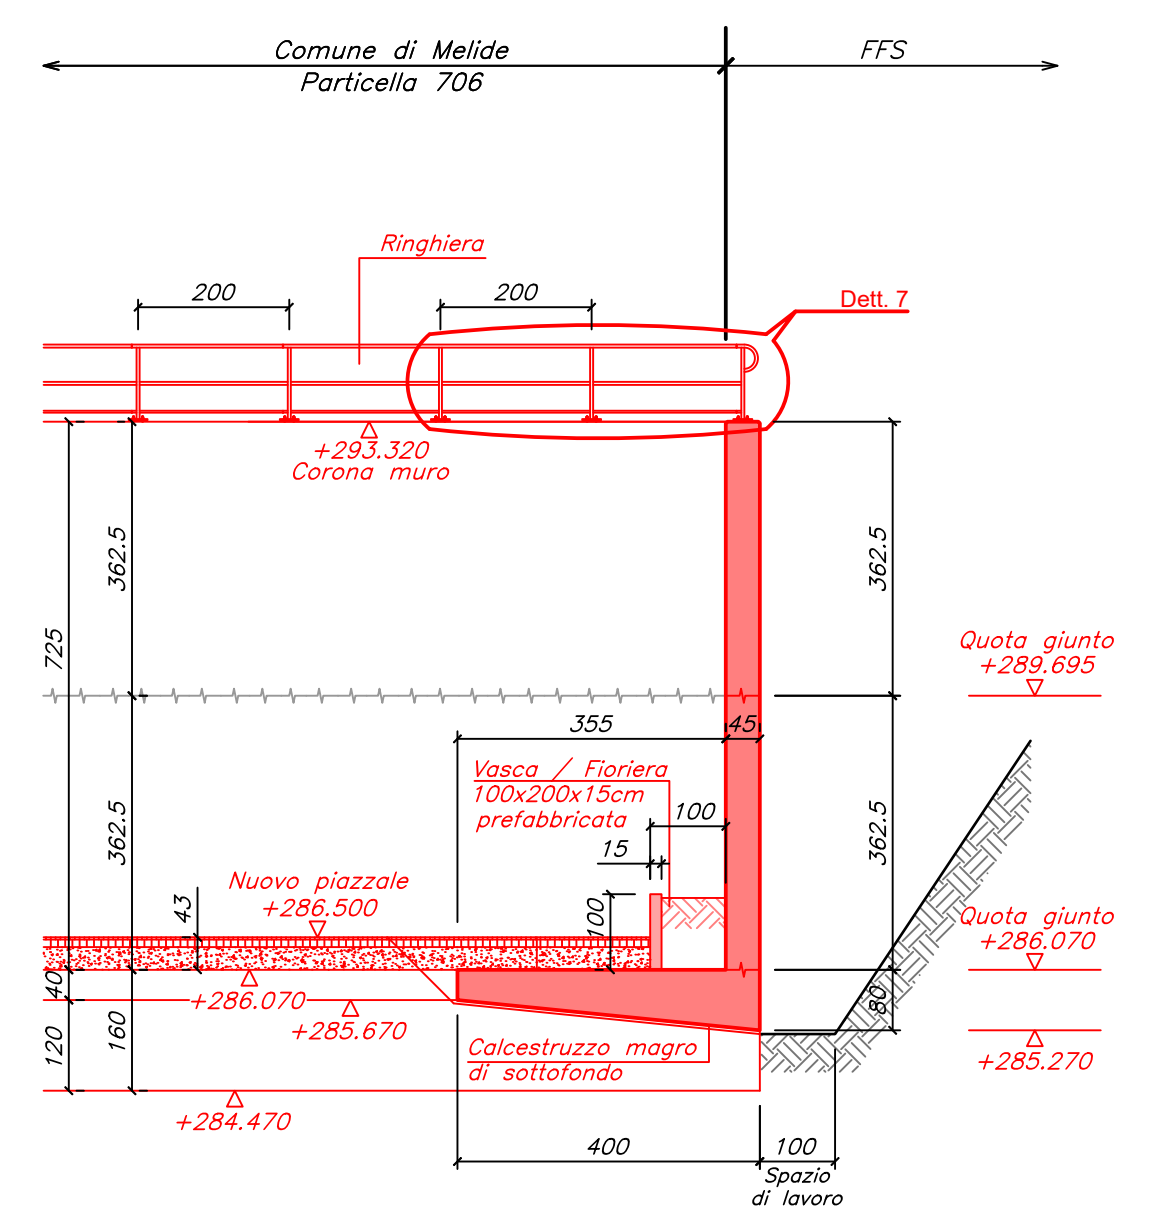

Sezione F-F (1:50)

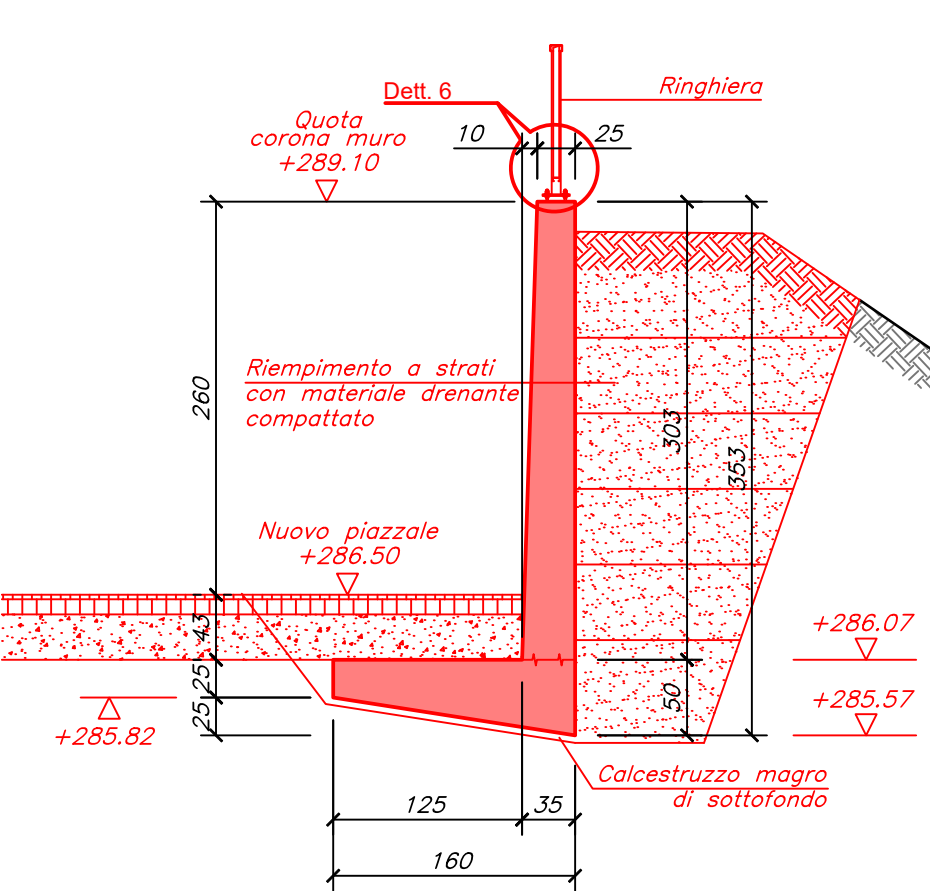


Sezione G-G (1:100)

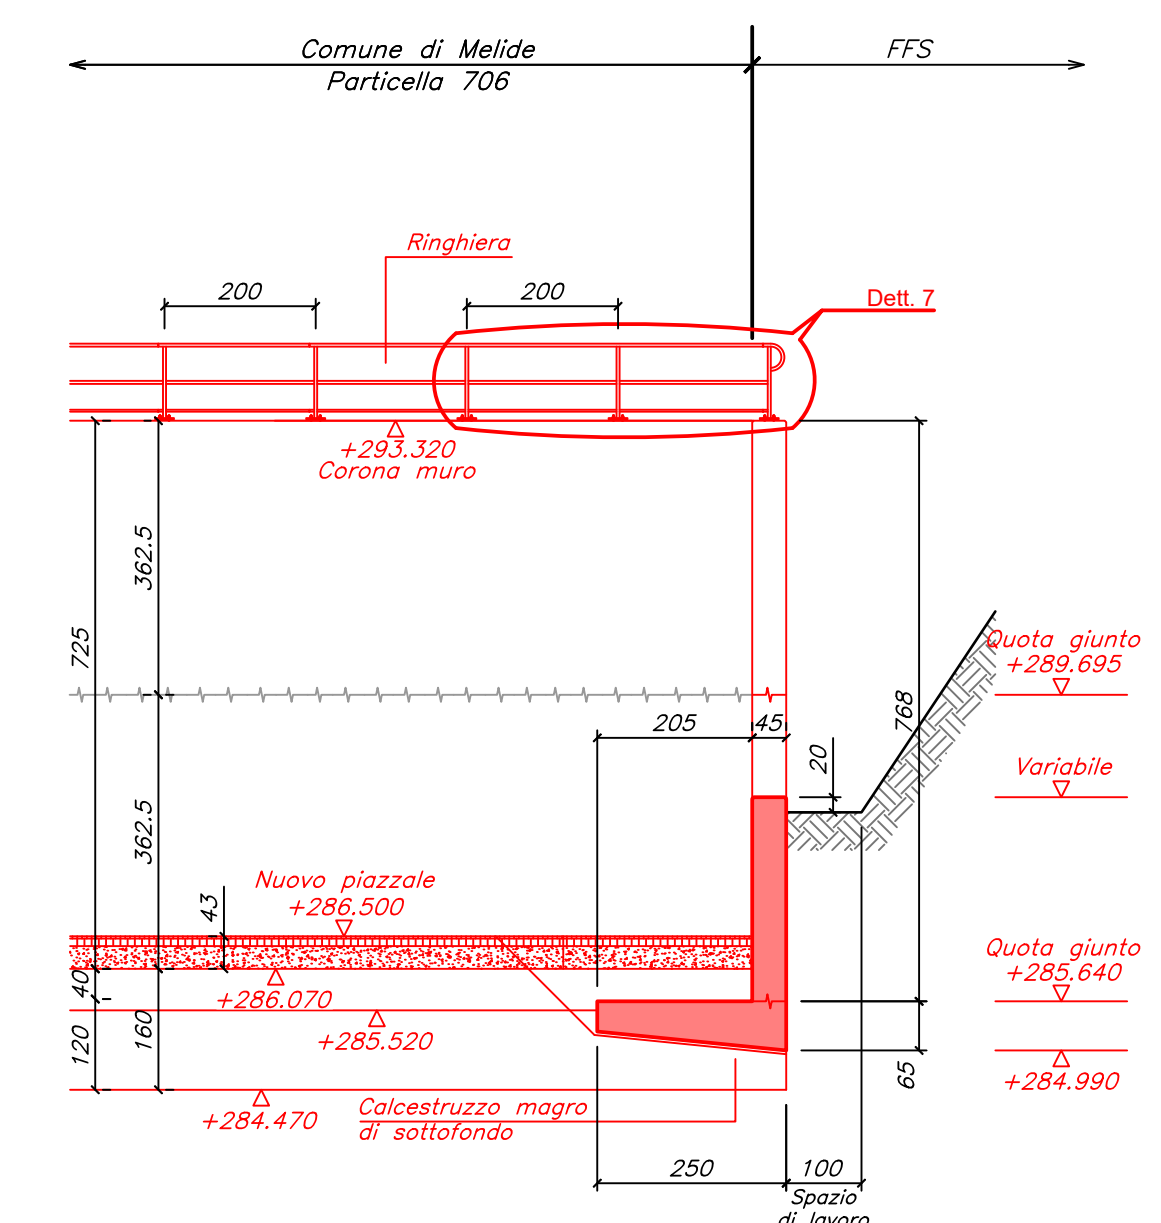


• CASSERATURA LATO INTERNO PIAZZALE DA REALIZZARE CON CASSERO FACCIA A VISTA 4.1.4.


Dettaglio 1 (1:10)

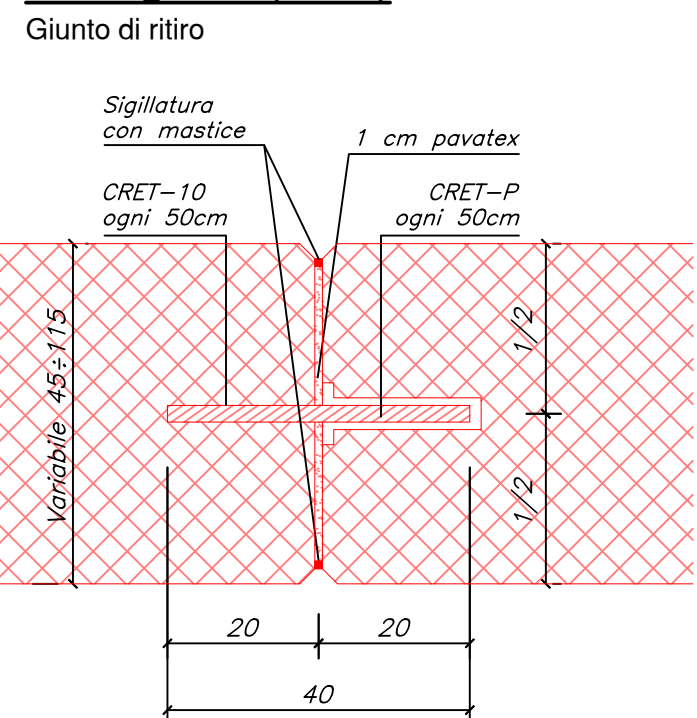


Dettaglio 3 (1:10)

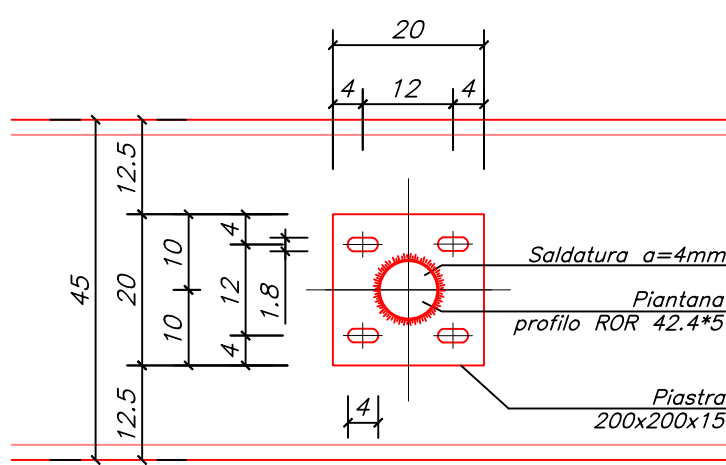


Dettaglio 4 (1:10)

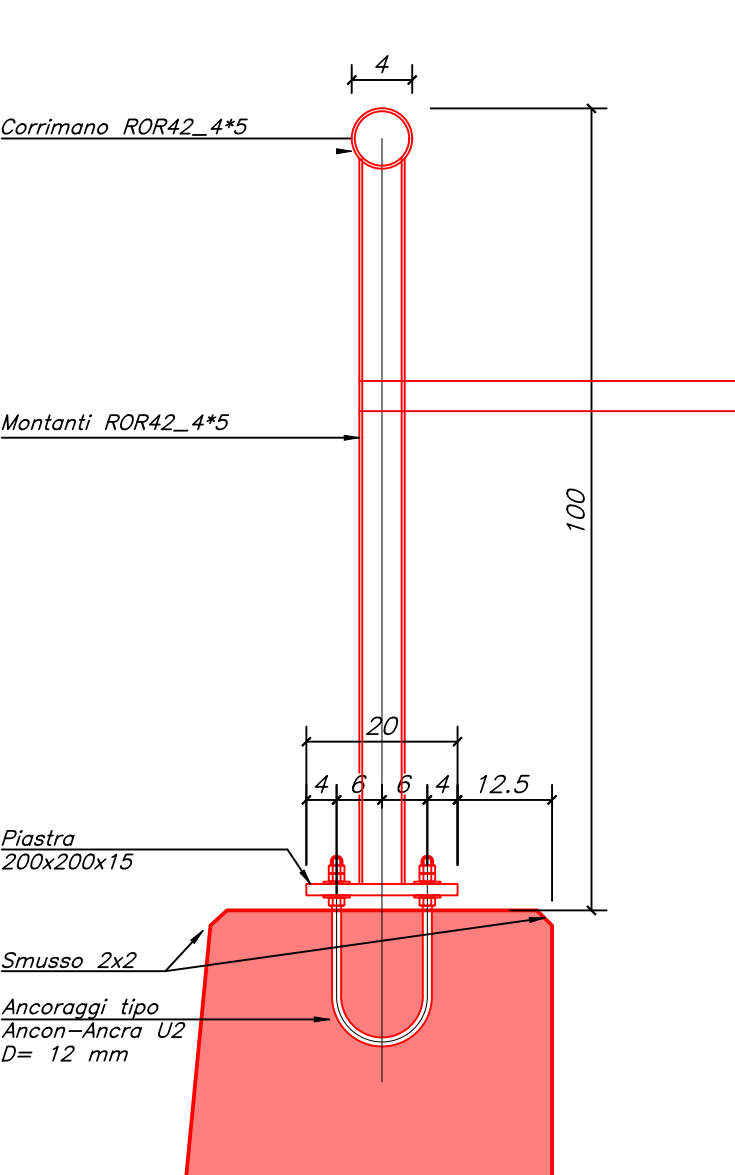


Dettaglio pavimentazione (1:20)

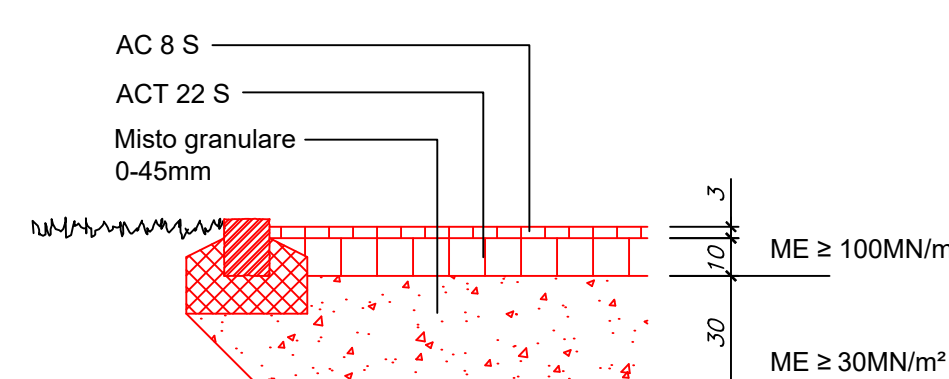


Dettaglio 2 (1:10)

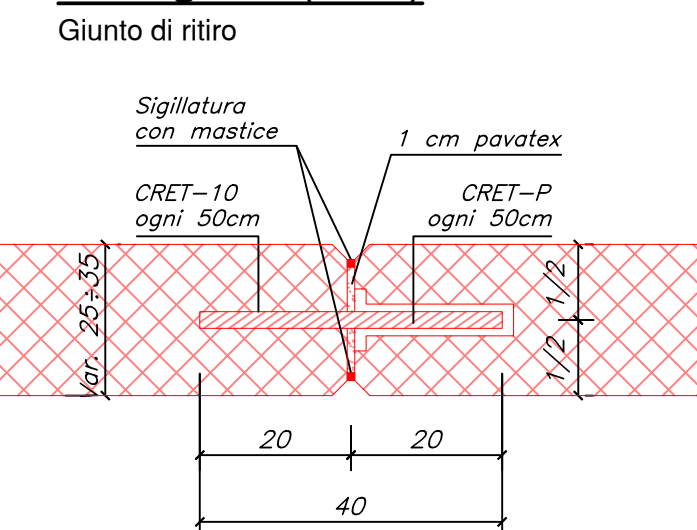


Vista dettaglio 7 (1:20)

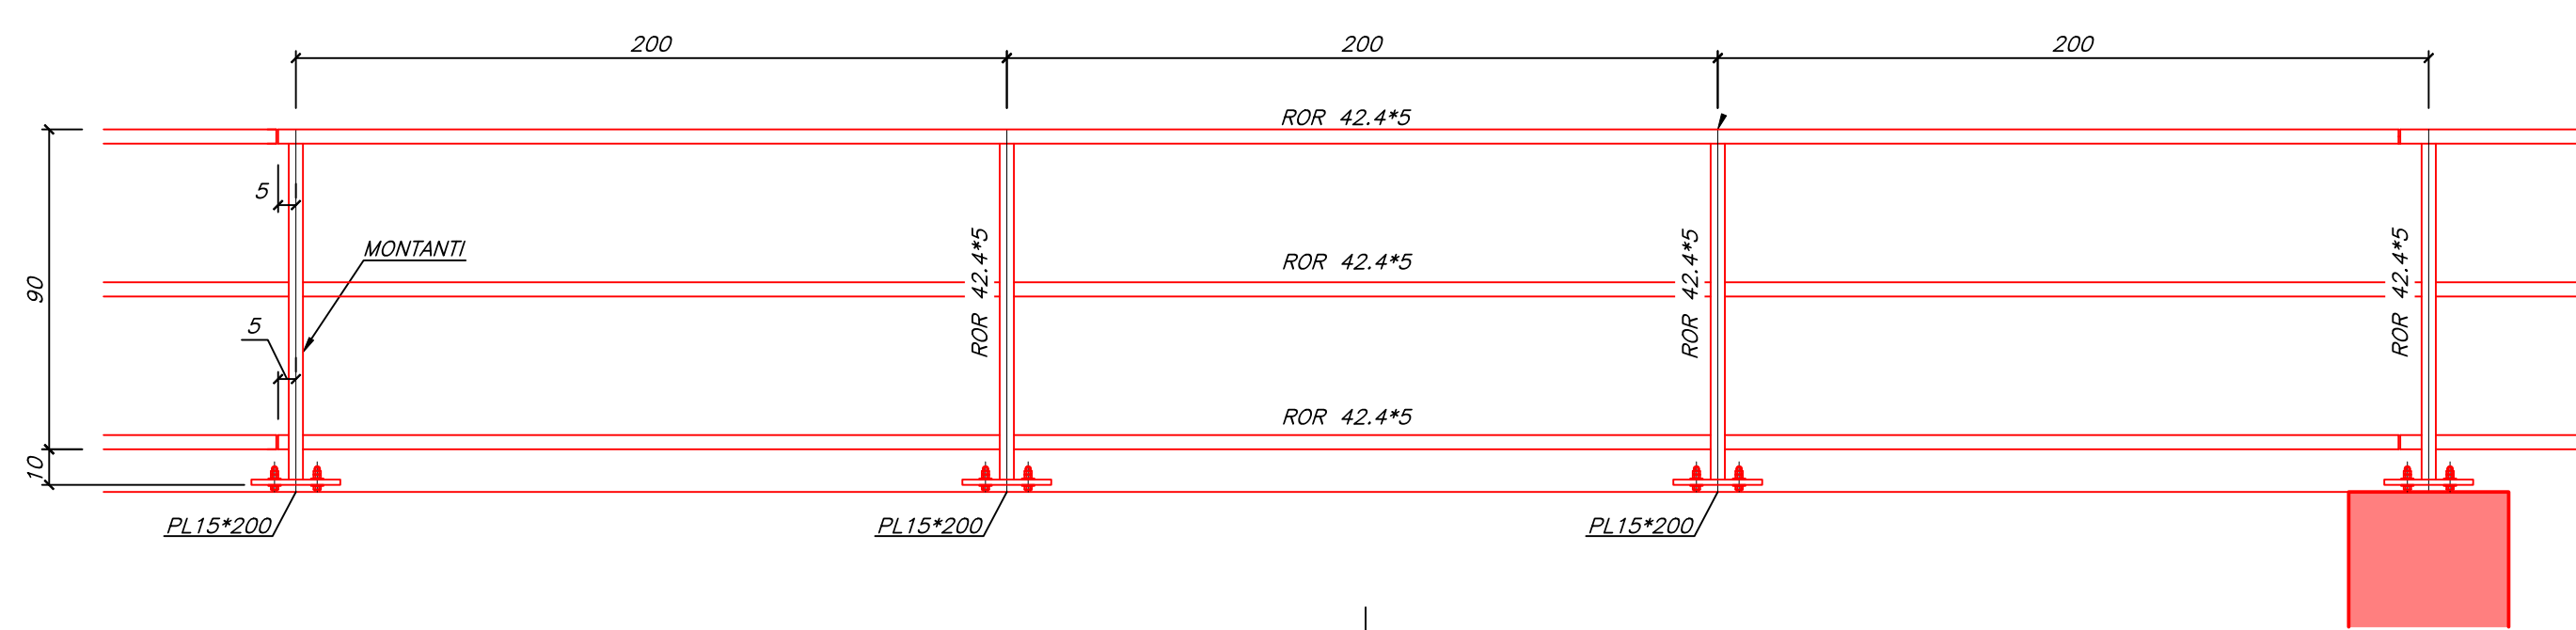

Sezione D-D Demolizione muro (1:100)

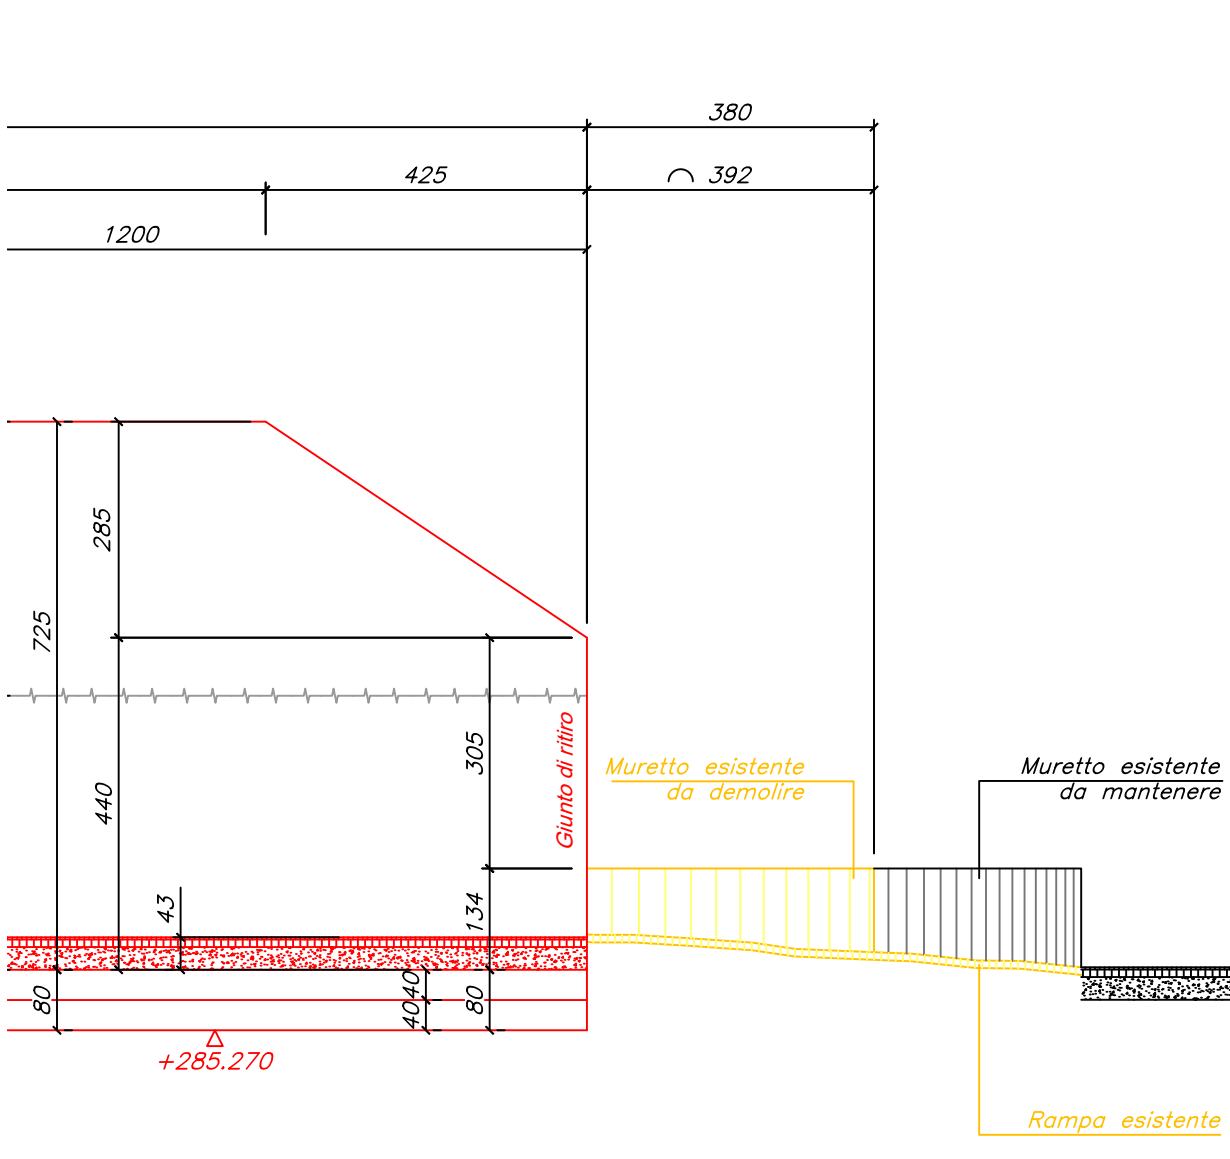


Sezione D-D (1:100)

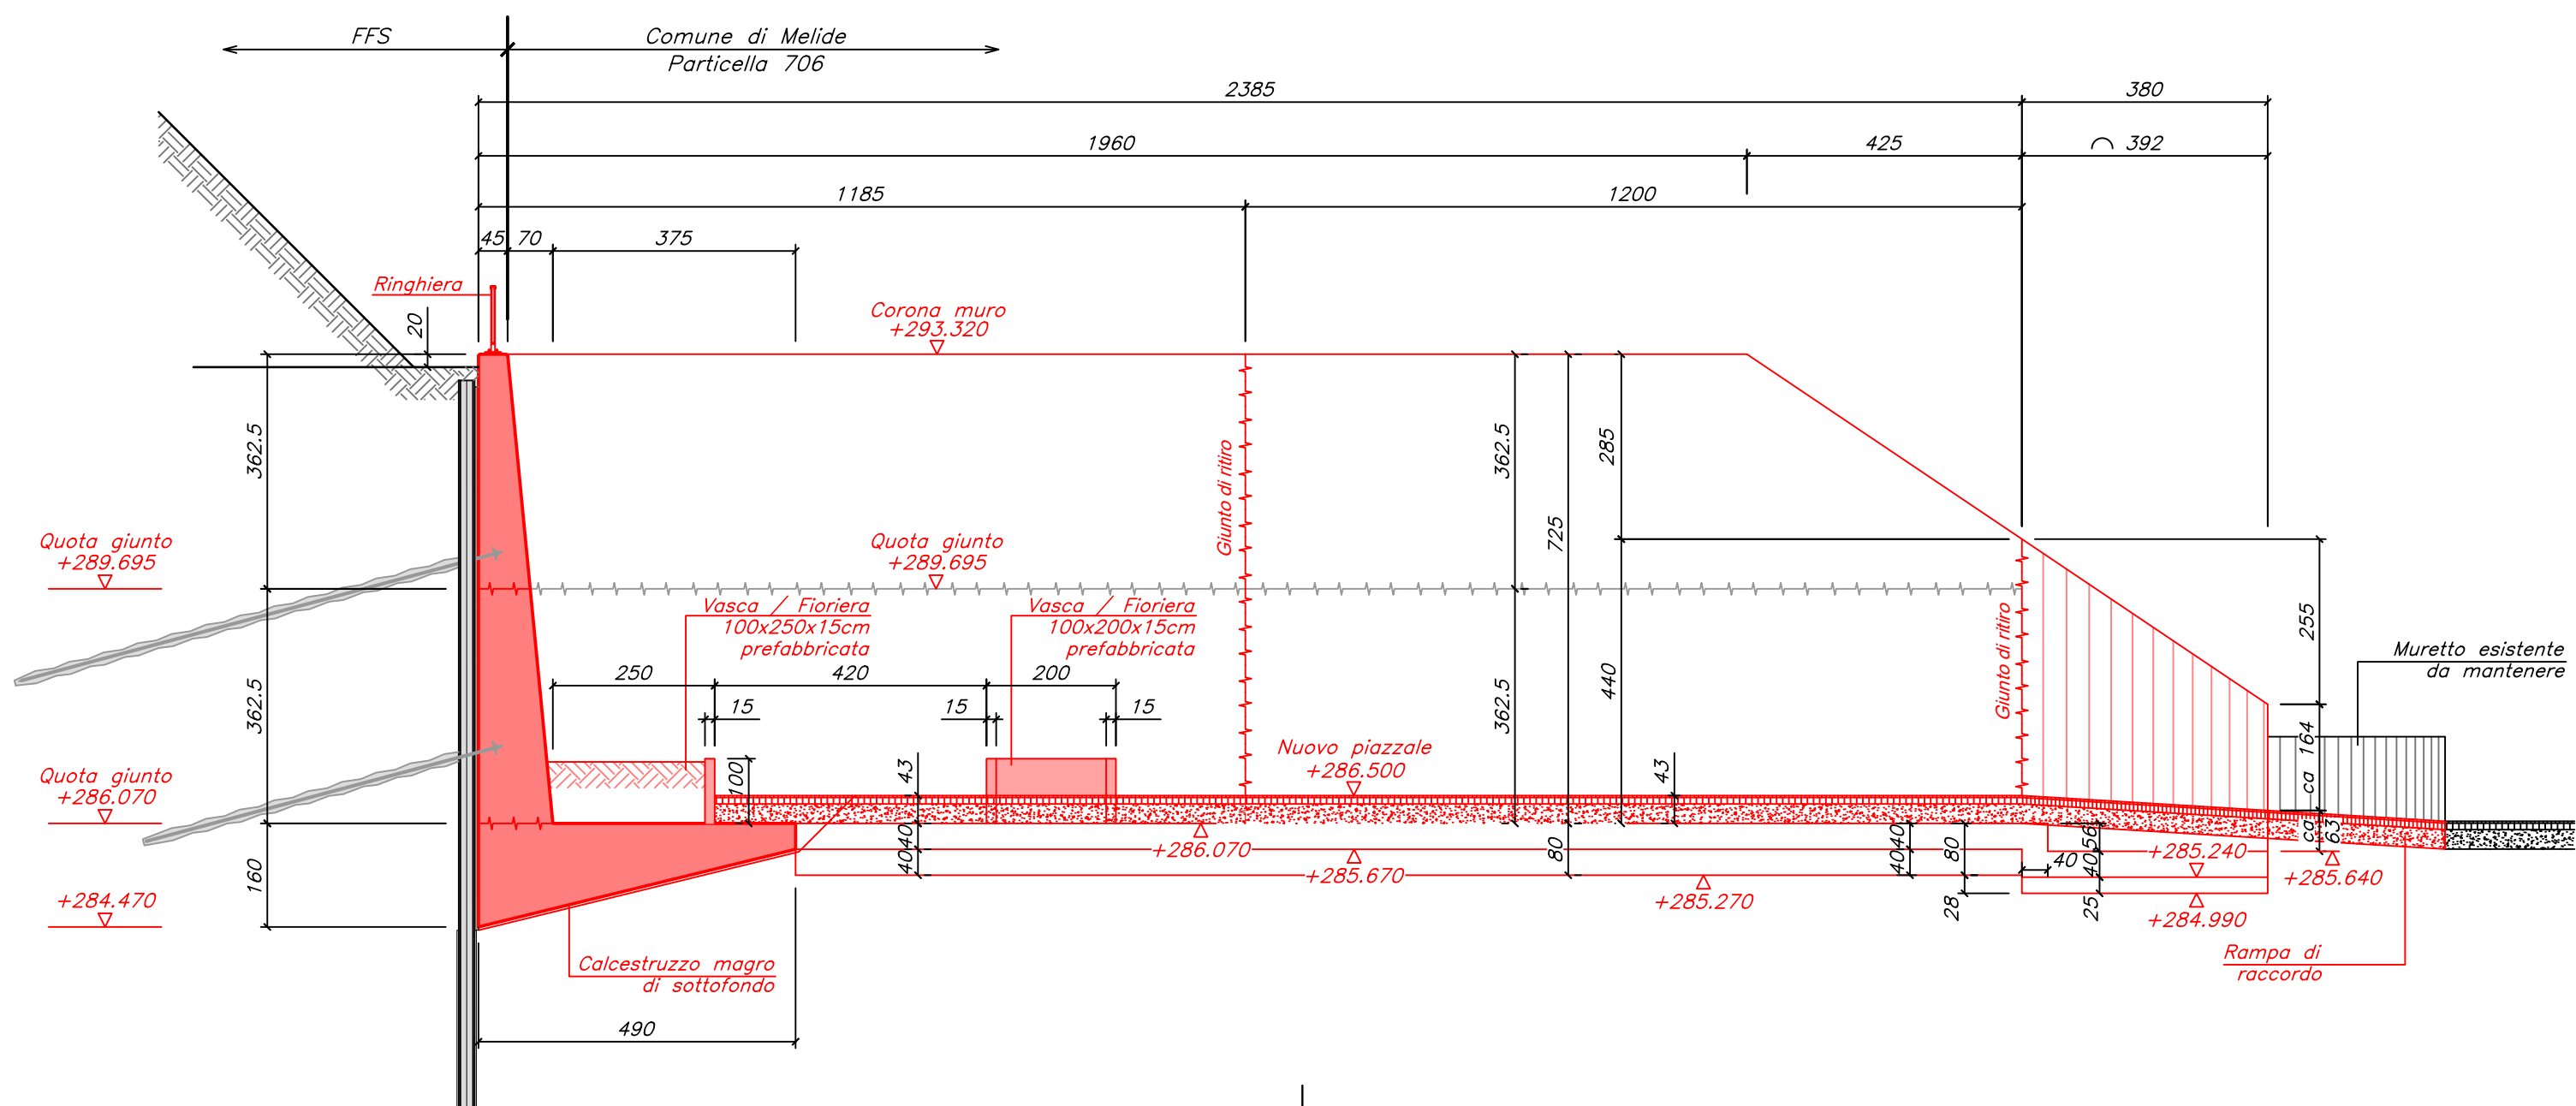

Linea: 600
Definizione: Tratta: Lugano - Paradiso - Melide
Km : 184.100 - 185.700
Cantone (i): Ticino
Comune (i): Lugano - Melide
Progetto: Linea 600 - San Salvatore
Opere di protezione

ISP-Nr.: 1146772

Fase: Piano dell'opera eseguita

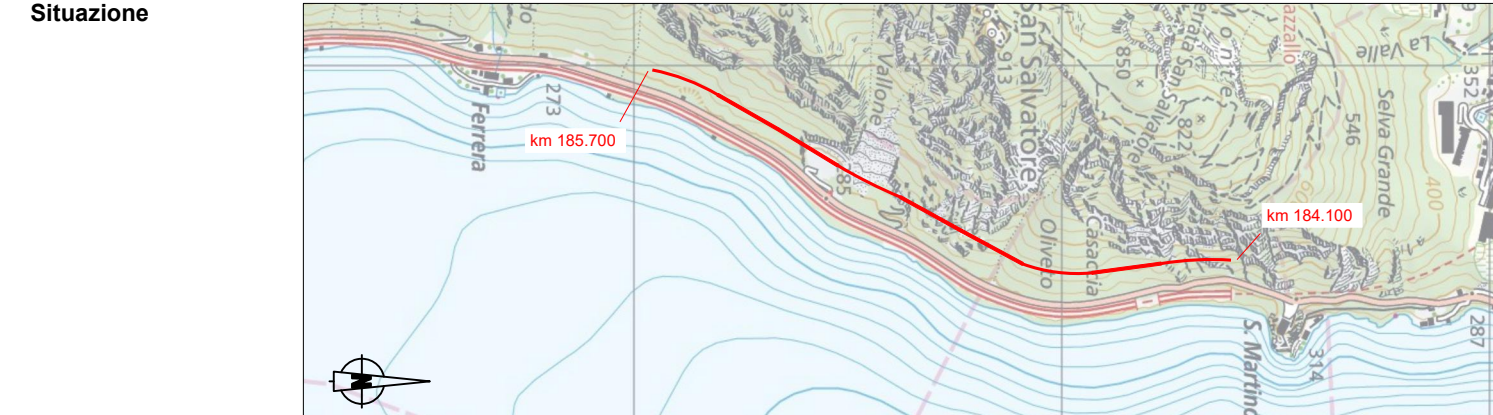

Firme
Capo progetto FFS
Reparto/OE: FFS-I-PJ-MP-OL-BEL2
Nome: Massimo Ferrari
Data: 20.01.2020
Progettista
Azienda: Consorzio Paradiso
Nome: Massimo Ferrari
Data: 20.01.2020
Firma

SBB CFF FFS

**Opere di protezione San Salvatore
Interventi Particella 706**

Piano cassero

Linea: 600
FFS, Infrastruttura
Via Pedemonte 7, 6500 Bellinzona

Km: 185.630 - 185.700

Piano no. 2594-i-049A
Indice: Disegnato: Via. Controllato: Via. Visto: Via.
A. 15.01.24 PB. 15.01.24 GL. 15.01.24 GL.
Modifica n. 1
Nome del File:
Formato: 59.4 x 126.0
Creato in base ai dati della misurazione ufficiale e della FFS.
© Con autorizzazione SBB CFF FFS. I dati del presente documento sono di proprietà della FFS. L'usatura postuma e la completezza delle coordinate sono garantite.