


Situation 1:250

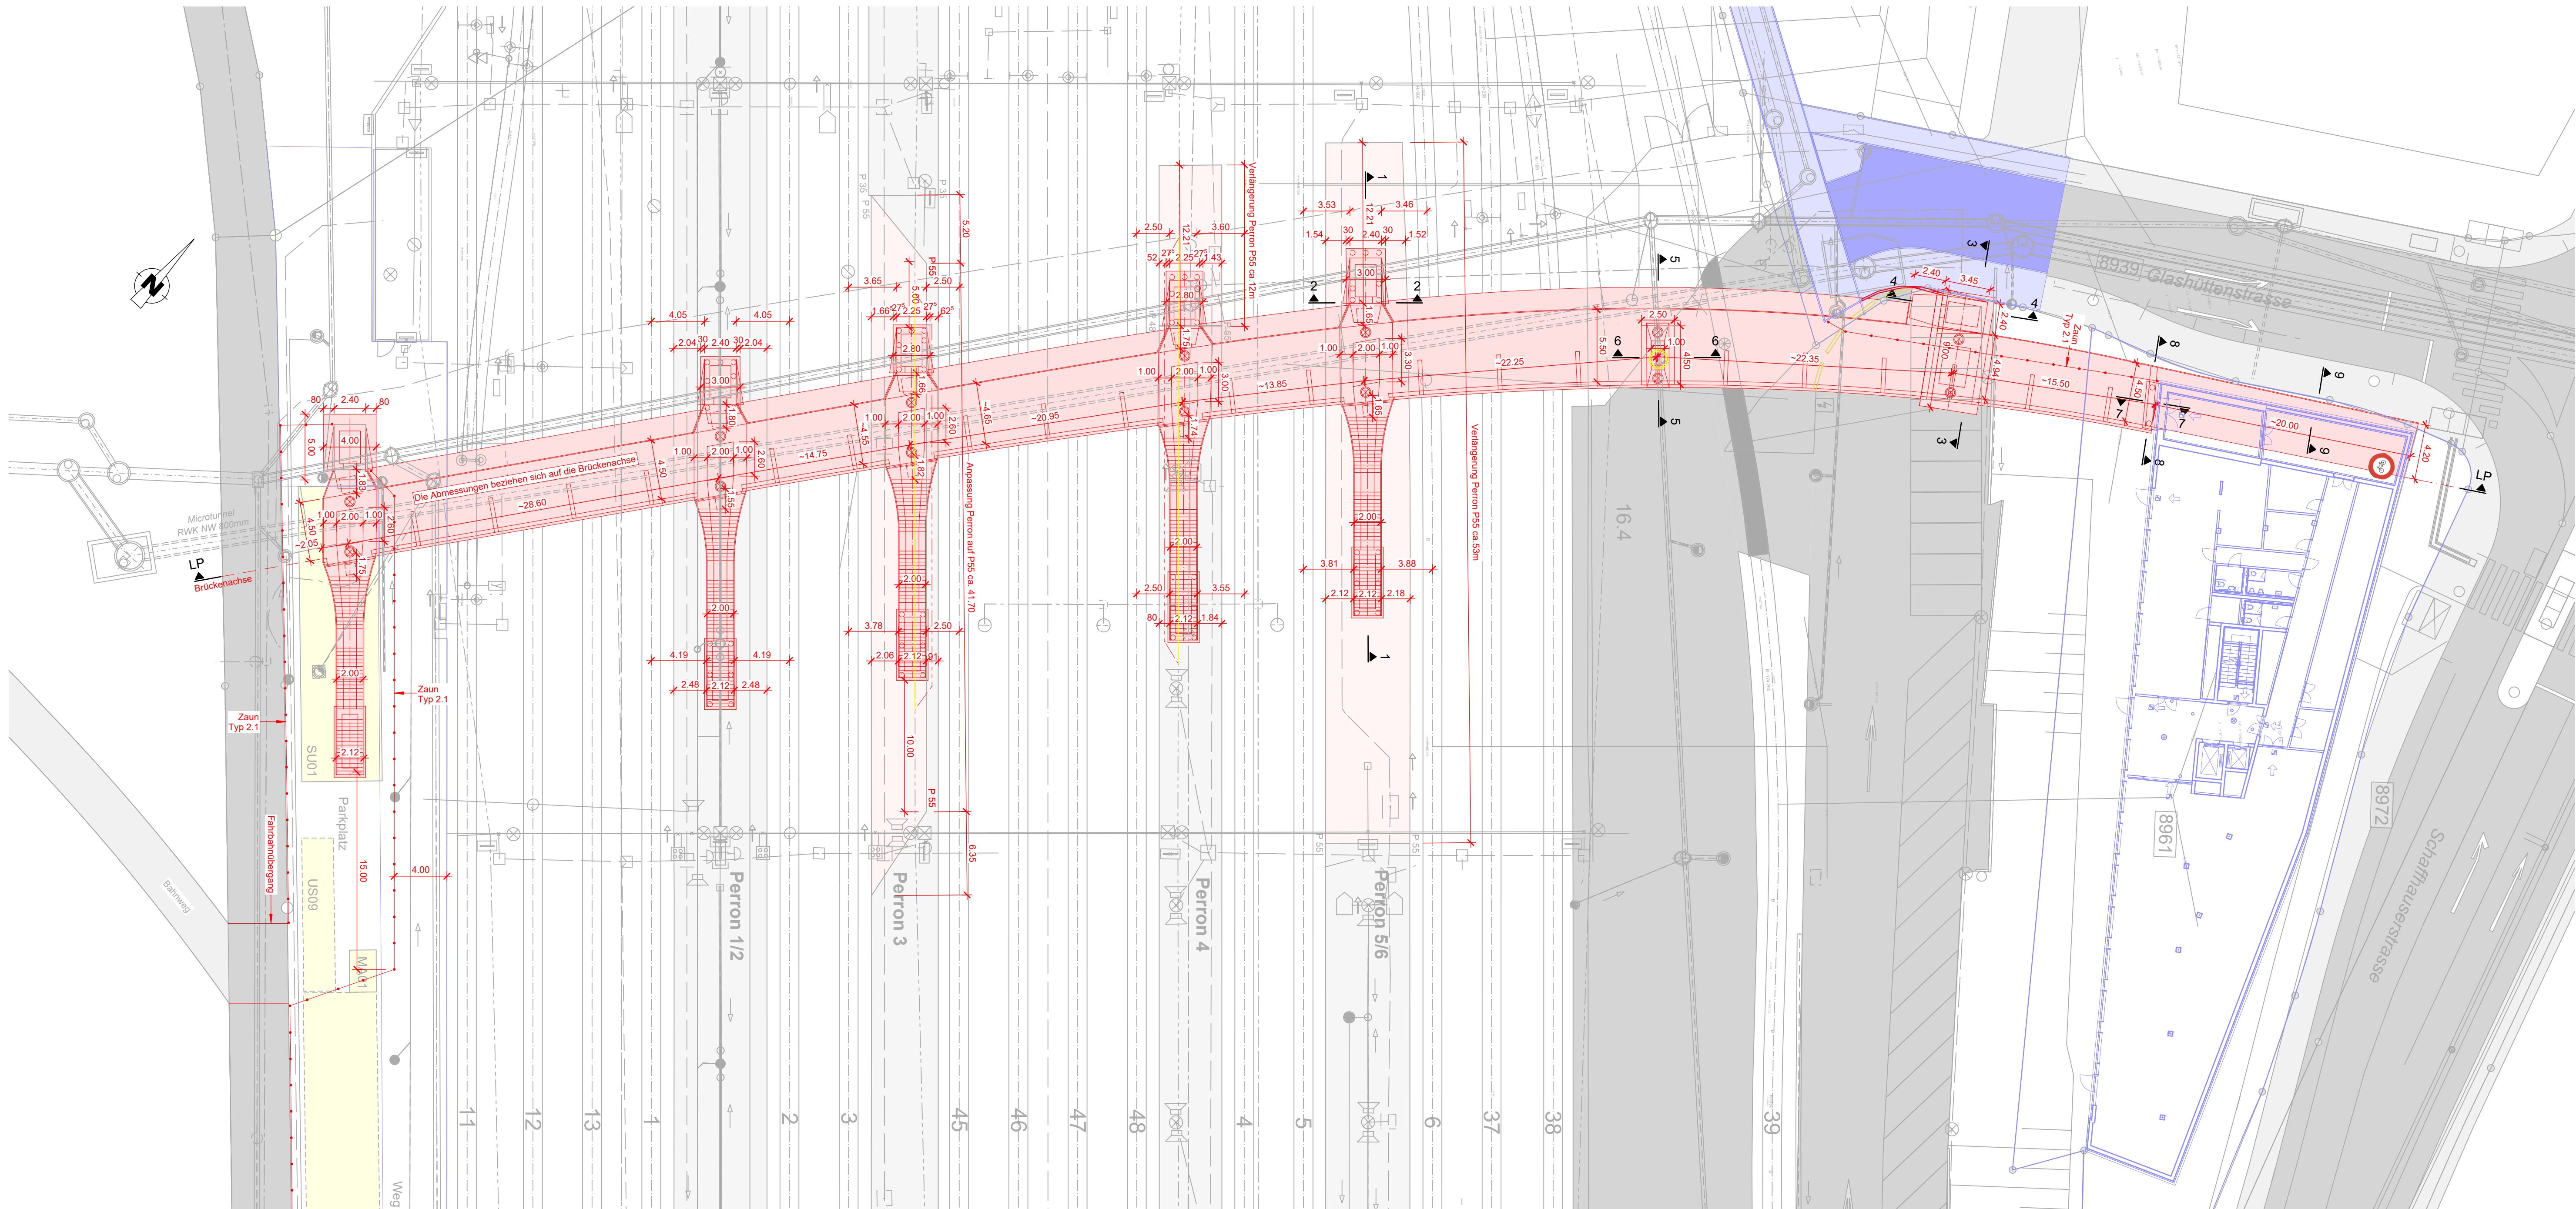

Legende

- Neubau
- Abbruch / Rückbau
- Bestand
- Drittprojekt

Betonsorten:

- Beton allgemein: G (T4) C30/37, XC4, XD3, XF4, D_{max} 32, Cl 0.10, C3
- AAR-Beständigkeit gem. SIA 2042: Präventionsklasse P2 hoher Frost-Tausalzstand
- Beton Bohrfähigkeit: P2 C28/30, D_{max} 32, Cl 0.10, F5, gemäss SIA 267
- AAR-Beständigkeit gem. SIA 2042: Präventionsklasse P2 hoher Frost-Tausalzstand
- Unterlagsbeton: CEM I, 150 kg/m³, D_{max} 32

Schalung:

- Sichtbare Schalung: Typ 4.4
- Nicht sichtbare Schalung: Typ 2.1
- Alle sichtbaren Kanten sind mit Dreikantenleisten 20 mm x 20 mm zu brechen
- Sichtbetonklasse 3 nach Merkblatt Cementsuisse MB02: hohe Anforderungen
- Betonoberflächenklasse BOK 3 nach SIA 118/262
- Nachbehandlungsklasse NBK 4
- Mauerkronen sind mit 1% Gefälle auszubilden

Oberflächenschutz Betonbauteile:

- Tiefenhydrophobierung und Graffitienschutz
- Alle horizontalen Betonoberflächen ohne Mörtelbeigabe abtalschieren.
- Betonanschlussflächen müssen aufgeraut und sauber sein. Sie sind bis zur Sättigung zu wässern.
- Ebenheit der Oberfläche, Toleranz gem. SIA 414 x 0.5
- Abdecken der Mörtel- und Betonoberfläche zur Verhinderung von vorzeitigem Austrocknen mittels Polyethylenfolie.
- Wärme- und Kälteschutz für frisch eingebrachten Beton mittels Thermomatten.
- Sämtliche freiliegenden Oberflächen sind nach Rücksprache mit der BL nach dem Ausschaln während 7 Tagen abzudecken.
- Die Abdeck- / Isolationsmatten sind mit Holzbalken an die Betonoberfläche satt anzupressen, sodass keine Luftzirkulation zwischen Matte und Wand stattfinden kann.

Bewehrung:

- Bewehrungsstahl B500B
- Bewehrungsüberdeckung: Sichtbeton: 55 mm

Stahlbau:

- Stahl S355
- Sämtliche Stahlbauarbeiten, insbesondere Schweissnähte, sind in der Ausführungsklasse EXC 3 nach EN 1090-2 auszuführen
- Die Schweissnähte der vor Ort montierten Bauteile müssen auf der Baustelle gestrahlt, grundiert und beschichtet werden.
- Applikationshalle Bereich Freierland und Nordstrasse

Oberflächenschutzsystem Stahlbauteile:

- Korrosivitätskategorie C4 gem. SN EN ISO 12944
- Alle scharfen Kanten sind brauenreif zu brechen r = 3 mm
- Sandstrahlen SA 2 1/2 und Rauigkeit Grt 2-3
- Leichtes Sandstrahlen als Untergrundvorbereitung Sweepen
- 1 Grundierung aus 2 Komponenten Epoxy - Haftgrund EP, Nominalschichtdicke e = 80 µm
- 1 Zwischenbeschichtung aus 2 - Komponenten Epoxy EP, Nominalschichtdicke e = 160 µm
- 1 Deckanstrich 2 - Komponenten Polyurethanlack PUR, UV - beständig, Nominalschichtdicke e = 80 µm

Abdichtung:

- Flüssigkeitskunststoffabdichtung auf Stahlplatte
- Erdberührte horizontale und vertikale Arbeitsfugen werden mittels Fugenband abgeklebt.

Lagerung Brücke:

- Mageda Lasto Block Verformungslager oder glw.
- in der Regel: ø800 Typ B rund
- Ausnahme Haus T: ø350 Typ B rund

11.5

Stadt Bülach

Gehweg - Passarelle
über SBB - Gleise

Bülach Nord

Situation und Längenprofil 1:250

Auflageprojekt

Bauherrschaft

Andrea Spycher
Zuständige Stadträtin Umwelt & Infrastruktur
Stadt Bülach


Projektverfasser

Dirk Kauffeld
Leiter Umwelt & Infrastruktur
Stadt Bülach

Spyridon Sokolakis
Projektleiter
F. Preisig AG

FPREISIGAG BAUINGENIEURE UND PLANER HAGENHOLZSTRASSE 83B, CH-8050 ZÜRICH, T 044 308 85 85 ZÜRICH@PREISIGAG.CH, WWW.PREISIGAG.CH ZÜRICH, BERN, BUCHS SG, CHUR, LENZBURG, ST. GALLEN, WINTERTHUR			Datum	31.05.2023
			Gez.	mul
			Proj.	mid
			Vis.	sos
Masstab	1:250	CAD-Dateiname	Plannummer	
Format	105 / 60		1384-005.200-11.5	

Längsprofil 1:250

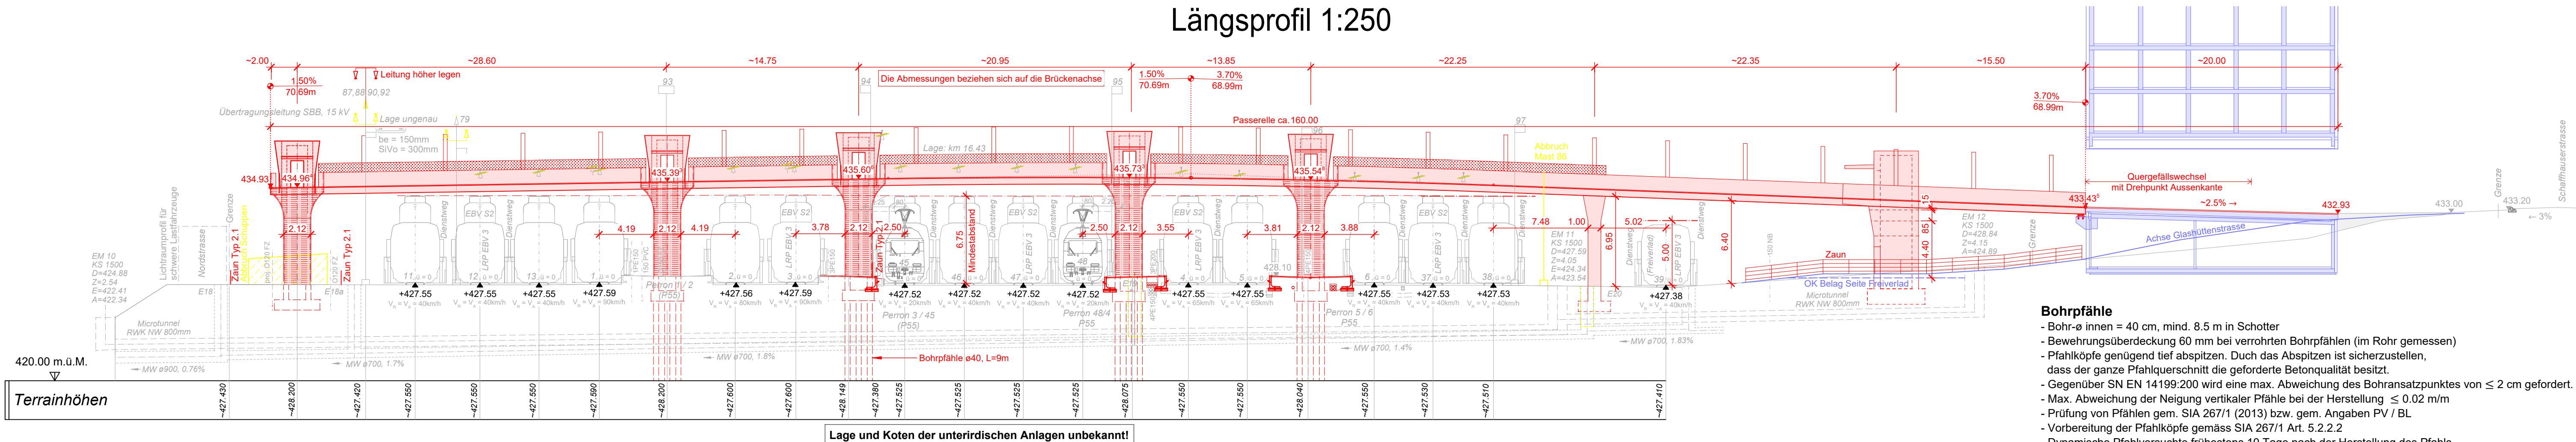

Lage und Koten der unterirdischen Anlagen unbekannt!

Allgemein gilt:

- Werkleitungen sind zu sondieren
- Sämtliche Masse sind am Bau zu kontrollieren und ggf. anzupassen
- Die Masttoleranzen gemäss SIA 262 Anhang A sind einzuhalten
- Massgebend für die Richtigkeit des Planes sind immer die angeschriebenen Koten und Masse unabhängig von ihrer zeichnerischen Darstellung. Differenzen sind der Bauleitung sofort mitzuteilen.
- Der Baingenieur ist vom Unternehmer rechtzeitig (24h vorher) aufzubieten für die Kontrolle der fertigverlegten Bewehrung.
- Die Verwendung von Betonzusätzen sind vom Ingenieur und der Bauleitung genehmigen zu lassen.
- Vorgegebene Winter- und Sommermassnahmen sind einzuhalten.
- Alle Bauteile gemäss Erdungskonzept erten.