


Gehweg - Passarelle über SBB - Gleise

Bülach Nord

Übersicht Beleuchtung

Ausführungsprojekt

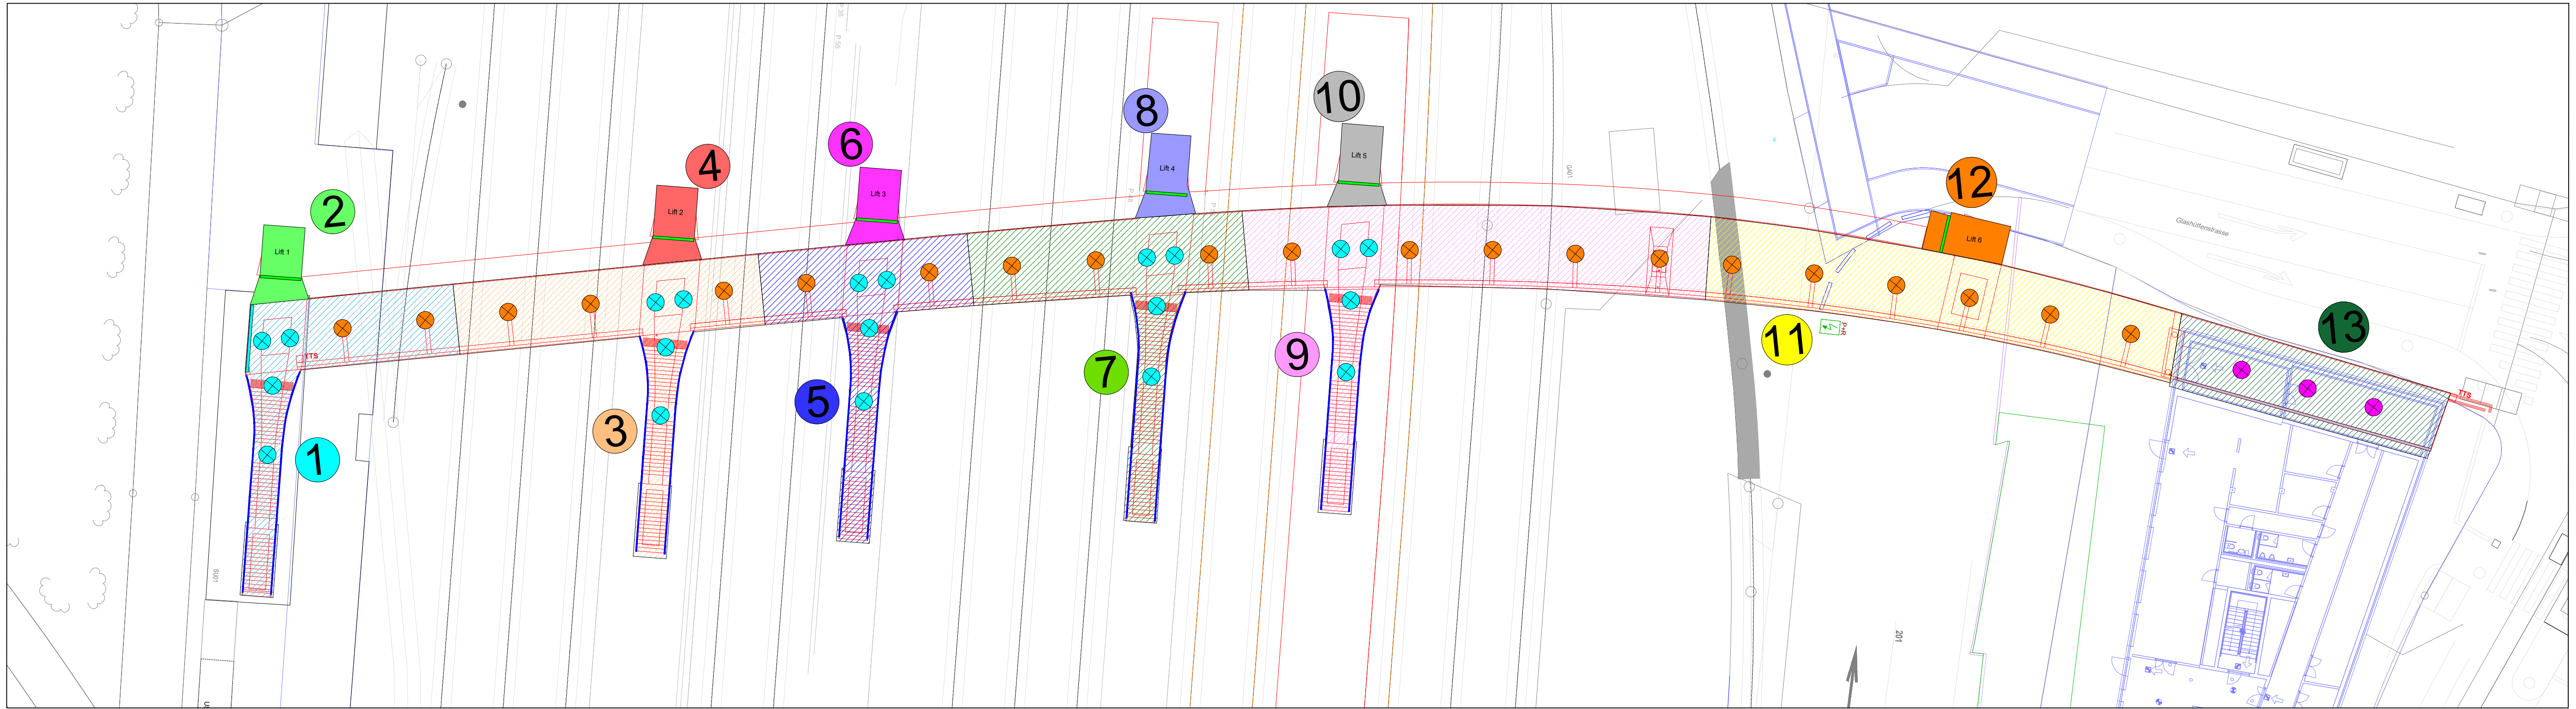

	Bezeichnung	Speisung	Steuerung	Beleuchtungstyp	Lichtfarbe	Eigentum	Betrieb/Unterhalt/Ersatz/Kosten
Zone 1	Treppenaufgang Platz auf Passarelle / Passarelle / Platz	EKZ / EKZ / EKZ	EKZ / EKZ / EKZ	Handlaufleuchten / Kandelaber "Prolight", Linearleuchten / Murten Leuchten	3000K / 3000K / 3000K	Stadt / Stadt / Stadt	Stadt / Stadt / Stadt
Zone 2	Lifanlage / Beleuchtung Vordach Lift	EKZ / EKZ	Stadt / EKZ	Linearleuchten	3000K	Stadt	Stadt / Stadt
Zone 3	Treppenaufgang Perron Gleis 1/2 auf Passarelle / Passarelle / Perron	EKZ / EKZ / SBB	SBB / EKZ / SBB	Handlaufleuchten / Kandelaber "Prolight", Linearleuchten / Murten Leuchten	3000K / 3000K / 3000K	Stadt / Stadt / SBB	SBB / Stadt / SBB
Zone 4	Lifanlage Gleis 1/2 / Beleuchtung Vordach Lift	EKZ / EKZ	Stadt / SBB	Linearleuchten	3000K	Stadt / Stadt	Stadt / Stadt
Zone 5	Treppenaufgang Perron Gleis 3/4/5 auf Passarelle / Passarelle / Perron	EKZ / EKZ / SBB	SBB / EKZ / SBB	Handlaufleuchten / Kandelaber "Prolight", Linearleuchten / Murten Leuchten	3000K / 3000K / 3000K	Stadt / Stadt / SBB	SBB / Stadt / SBB
Zone 6	Lifanlage Gleis 3/4/5 / Beleuchtung Vordach Lift	EKZ / EKZ	Stadt / SBB	Linearleuchten	3000K	Stadt / Stadt	Stadt / Stadt
Zone 7	Treppenaufgang Perron Gleis 4/4/8 auf Passarelle / Passarelle / Perron	EKZ / EKZ / SBB	SBB / EKZ / SBB	Handlaufleuchten / Kandelaber "Prolight", Linearleuchten / Murten Leuchten	3000K / 3000K / 3000K	Stadt / Stadt / SBB	SBB / Stadt / SBB
Zone 8	Lifanlage Gleis 4/4/8 / Beleuchtung Vordach Lift	EKZ / EKZ	Stadt / SBB	Linearleuchten	3000K	Stadt / Stadt	Stadt / Stadt
Zone 9	Treppenaufgang Perron Gleis 5/6 auf Passarelle / Passarelle / Perron	EKZ / EKZ / SBB	SBB / EKZ / SBB	Handlaufleuchten / Kandelaber "Prolight", Linearleuchten / Murten Leuchten	3000K / 3000K / 3000K	Stadt / Stadt / SBB	SBB / Stadt / SBB
Zone 10	Lifanlage Gleis 5/6 / Beleuchtung Vordach Lift	EKZ / EKZ	Stadt / SBB	Linearleuchten	3000K	Stadt / Stadt	Stadt / Stadt
Zone 11	Passarelle zwischen Gleis 3/9 und Galerie	EKZ	EKZ	Kandelaber "Prolight"	3000K	Stadt	Stadt
Zone 12	Lifanlage Gleis 3/9 / Beleuchtung Vordach Lift	EKZ / EKZ	Stadt / EKZ	Linearleuchten	3000K	Stadt	Stadt
Zone 13	Galerie	EKZ	EKZ	Murten Leuchten / Linearleuchte	3000K / 3000K	Stadt / Stadt	Stadt

- Legende:
- Kleinkandelaber "Prolight"
 - Aufbauleuchten "Regent Murten" (AP), unterhalb Treppenaufgang
 - Aufbauleuchten "Regent Murten" (AP), Galerie
 - Linearleuchte (UP), Galerie
 - Linearleuchte vor Liftzugang (UP)
 - Linearleuchte auf Passarelle
 - Handlaufbeleuchtung "Model SBB", Einzelmodul (asymetrische Abstrahlung)

Zusammenfassung gem. Bespr. 01.12.2023 Abstimmung mit Objektvertrag

-Beleuchtung Vordach Lift BZU
Steuerung = SBB

-Beleuchtung Treppe BZU
Betrieb/Unterhalt/Ersatz/Kosten/Steuerung= SBB

-Bauwerk
Betrieb/Unterhalt/Ersatz/Rückbau/Kosten= Stadt

-Lifanlage
Betrieb/Unterhalt/Ersatz/Kosten= Stadt

Index	Bemerkungen, Änderungen	Gezeichnet	Geprüft	Freigabe
A	Aufmodellierung der Unterlagen für definitive Version PGV Abgabe	31.05.23 / rla		
B	Objektvertrag abstimmen/kordinieren mit der Elektroinstallation	01.12.23 / rla	01.12.23 / mwj	01.12.23 / glä
C				
D				

 ELEKTROINGENIEURE AG In der Luberzen 25 CH-8902 Urdorf Telefon 044-735 66 33 www.hdz.ch	Datum	01.12.2023
	Gez.	rla
	Proj.	cle
	Vis.	cle

Massstab	1:250	CAD-Dateiname	Plannummer
Format	105 / 30	6145-04-102.dwg	1384-005.200-13.2