


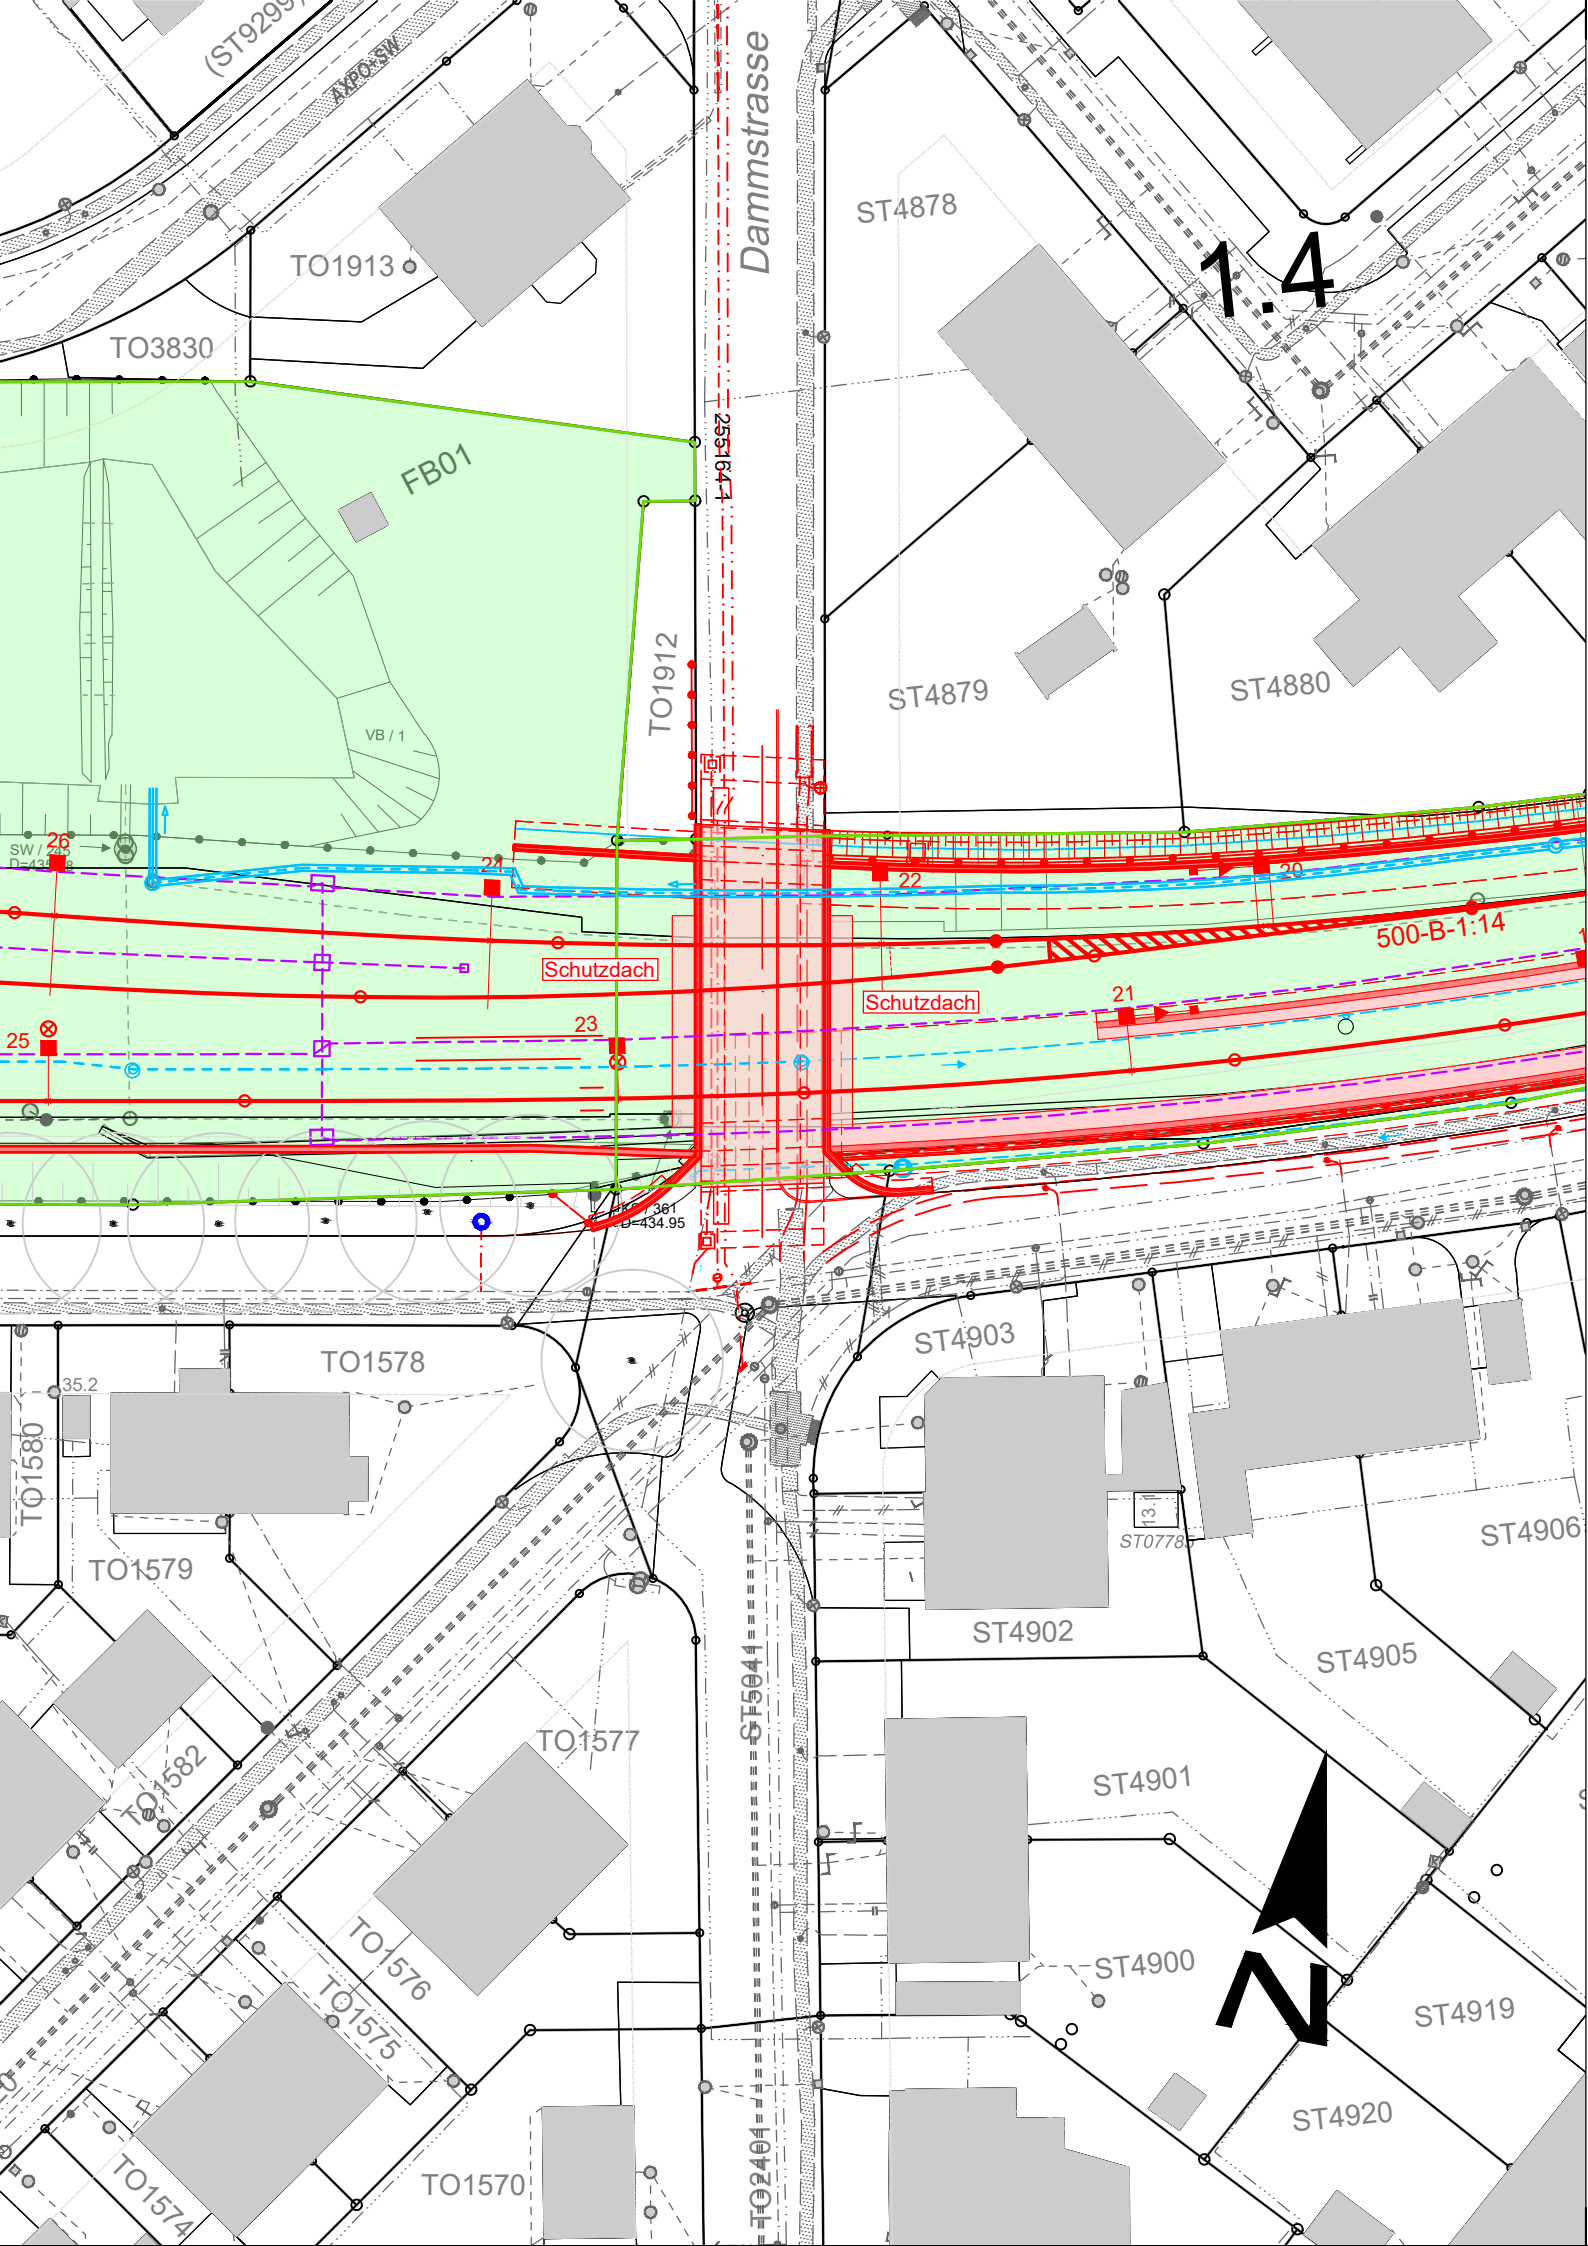

Legende

- Bestand
- Parzellengrenze SBB
- SBB Parzelle
- Projekt
- Projekt Dritte

Werkleitungen

- Mischabwasser
- Schmutzabwasser
- Meteorabwasser
- Elektro
- Telefon (Fernmeldeanlagen)
- Gas
- Fernwärme
- Fernsehen (Gem.-Antennen)
- Wasser

Projekt Werkleitungen Bahnbau

- Bahnabwasser Vollrohr
- Bahnabwasser Sickerrohr
- Bahnabwasser Sickergraben/Rinne
- Kabelanlagen

Impressum



c/o dsp Ingenieure + Planer AG
Zürichstrasse 4, 8610 Uster
T +41 44 905 88 88, www.dsp.ch

EBP Schweiz AG

Vertragsplan 1:500

Winterthur Töss

Ueberführung Dammsstrasse

Linie: 769

Km: 1.434

SBB, Infrastruktur
Vulkanplatz 11, 8048 Zürich



Plan Nr. PLAN-NR

Index	Erstellt	Vis.	Geprüft	Vis.	Freigabe	Vis.
rC00	29.04.25	CEL	29.04.25	AHU	29.04.25	CI

Filename:
MSZW_BP_A1_xx-xx-xx-xx_Vertragsplan_Ue_Dammsstrasse_rC00

Format: A3

Erstellt auf Basisdaten der amtlichen Vermessung und der SBB-Geodaten
© Geodaten swisstopo 5704003351 © Alle Rechte an diesem Dokument
stehen der SBB zu. Für die genaue Lage und die Vollständigkeit der
unterirdischen Anlagen besteht keine Gewähr.