

C O N V E N T I O N

entre la Direction du 1^{er} arrondissement des chemins de fer fédéraux, à Lausanne, d'une part,

et

la Commune de Neuchâtel, représentée par la Direction soussignée des Travaux publics, d'autre part.

Exposé.

La Commune de Neuchâtel construisant un raccordement de la route des Parcs avec les carrefours de Vauseyon et du Haut de Maillefer a demandé aux C.F.F. d'étudier le prolongement du tunnel du Gibet, sur la ligne Neuchâtel-Chaux de fonds, nécessaire pour le passage de ce raccordement sur la tête du tunnel côté Vauseyon. Ces travaux qui comprennent le prolongement du tunnel d'environ 14 mètres et la construction de deux nouveaux murs en aile destinés à soutenir les terrassements du chemin communal, seront exécutés suivant les plans indiqués ci-après qui font partie intégrante de la présente convention:

Profils en travers et plan No. 4557 C.F.F. du 9 avril 1919.

Profil-type, coupe et plan No. 4558 C.F.F. du 10 avril 1919.

Ces plans ayant été approuvés par les autorités fédérales, la Direction du 1^{er} arrondissement des chemins de fer fédéraux se déclare prête à pourvoir à l'exécution des travaux, pour le compte de la Commune de Neuchâtel, aux conditions suivantes:

Art. 1^{er}.

a) Les travaux seront mis au concours et adjugés ensuite d'entente entre la Commune de Neuchâtel et les Chemins de fer fédéraux.

b) La surveillance et la direction des travaux seront exercés exclusivement par les organes des C.F.F. qui pourvoiront à l'établissement des situations mensuelles et du décompte final.

c) Les paiements aux entrepreneurs et toutes les autres dépenses que les C.F.F. auront à faire pour l'exécution de ces travaux feront l'objet d'un compte de tiers, dont le montant sera majoré de 10 % pour frais généraux d'étude et de surveillance.

d) La Commune de Neuchâtel remboursera ces dépenses aux C.F.F. dans le mois qui suivra la reconnaissance des travaux.

Art. 2.

Les C.F.F. supporteront la responsabilité des accidents qui pourraient survenir durant ces travaux moyennant une majoration supplémentaire de 3 % calculée sur le montant total du compte de tiers, majoré comme il est dit à l'art. 1^{er}, lettre c.

Toutefois, la Commune de Neuchâtel restera responsable des accidents qui pourraient se produire par la faute de ses employés ou du fait des travaux qu'elle exécute elle-même à proximité de ce chantier.

Art. 3.

L'entretien de ces maçonneries incombera dans la suite aux C.F.F., à partir de la reconnaissance définitive des travaux.

Art. 4.

La Commune de Neuchâtel pourvoira à l'écoulement rationnel des eaux de ces nouvelles routes, qui ne devront pas s'écouler sur la tête du tunnel ou sur les talus C.F.F.

Art. 5.

Après l'exécution des travaux, la Commune de Neuchâtel fera procéder à ses frais, d'entente avec les organes des C.F.F., à l'abornement des parcelles à transférer au chapitre de la Commune. Elle remettra aux C.F.F. un plan de division original de ces terrains.

La Commune de Neuchâtel payera ces terrains aux C.F.F. au prix qui sera convenu ultérieurement.

Ces opérations seront liquidées en dehors du compte de tiers mentionné plus haut.

Fait en double à Neuchâtel et Lausanne, le 8 septembre 1919.

Pour la Commune de Neuchâtel:
Le Directeur des Travaux publics,

Berthoud.

Pour la Direction
du 1^{er} arrondissement
des chemins de fer fédéraux:

T. Berthoud.

— C.F.F. —

1^{er} arrondissement.

Ligne Neuchâtel - Col-des-Roches.

Commune de Neuchâtel.

Routes Pavez - Vaudey - Maillefer.
Prolongement du tunnel du Gibet.

Profils en travers.

1:100

Plan de situation.

1:1000




Reconnu comme annexe et partie intégrante
de la convention du 8 septembre 1919.


Pour la Commune
de Neuchâtel.

Pour la Direction du 1^{er} Arrondissement
des Chemins de fer fédéraux

[Signature]

[Signature]

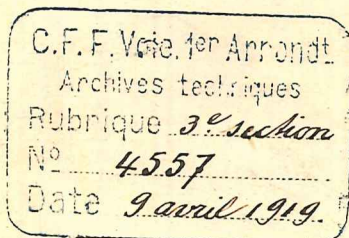

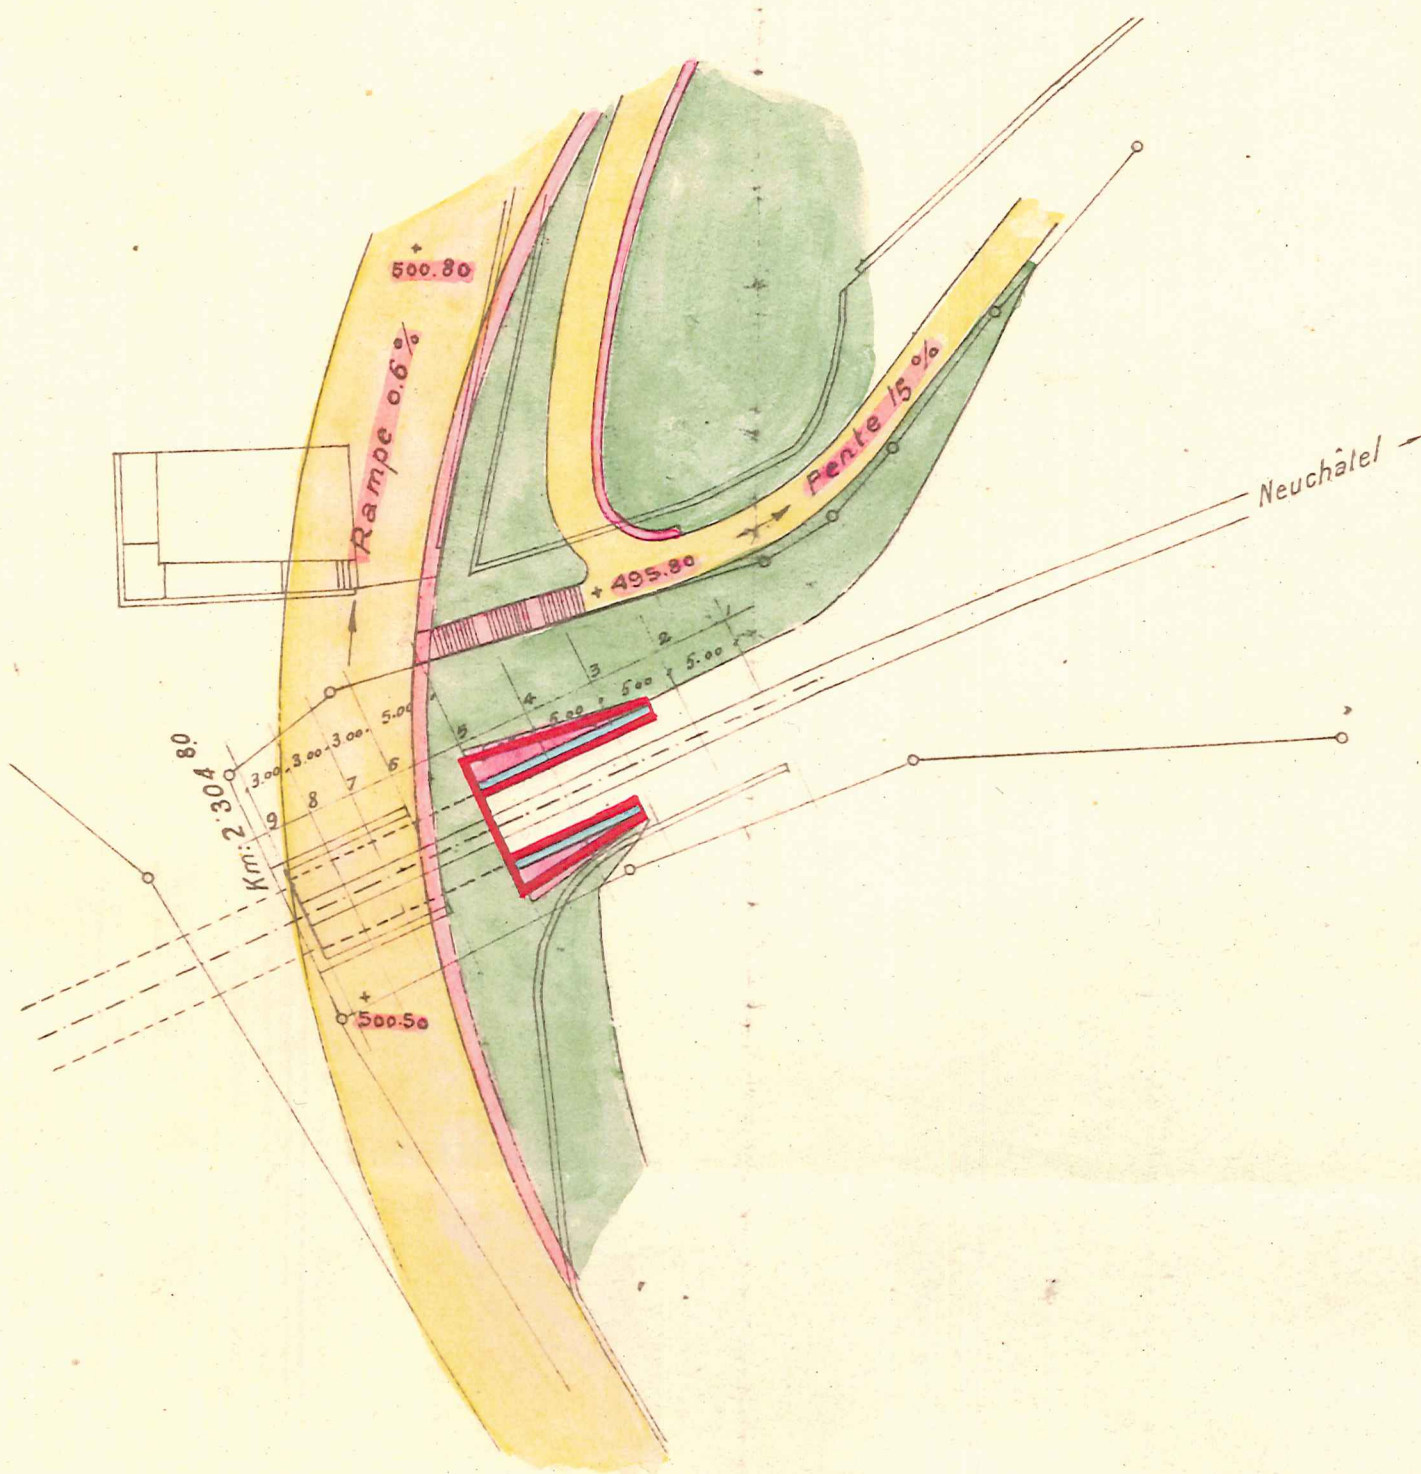

Plan de Situation.

Echelle 1:500.

Neuchâtel Février 1919.

— C.F.F. —

1^{er} arrondissement.

Ligne Neuchâtel - Col des Roches.

Commune de Neuchâtel.

Routes Pato - Vauseyon - Maillefer.


Prolongement du tunnel du Gibet.

— Coupe longitudinale et plan. —

1:100

— Profil-type. —

1:50

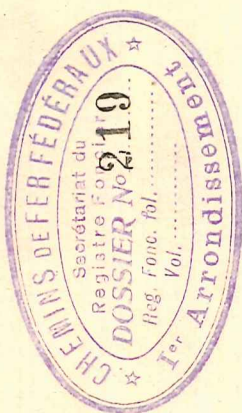

Reconnu comme annexe et partie intégrante
de la convention du 8 septembre 1918.

Pour la Commune
de Neuchâtel.

Pour la Direction du 1^{er} Arrondissement
des Chemins de fer fédéraux


[Signature]

[Signature]

C.F.F. Voie. 1^{er} Arrondt.
Archives techniques
Rubrique 3^e section
No 4558
Date 10 avril 1919.

— Profil-type. —

1:50

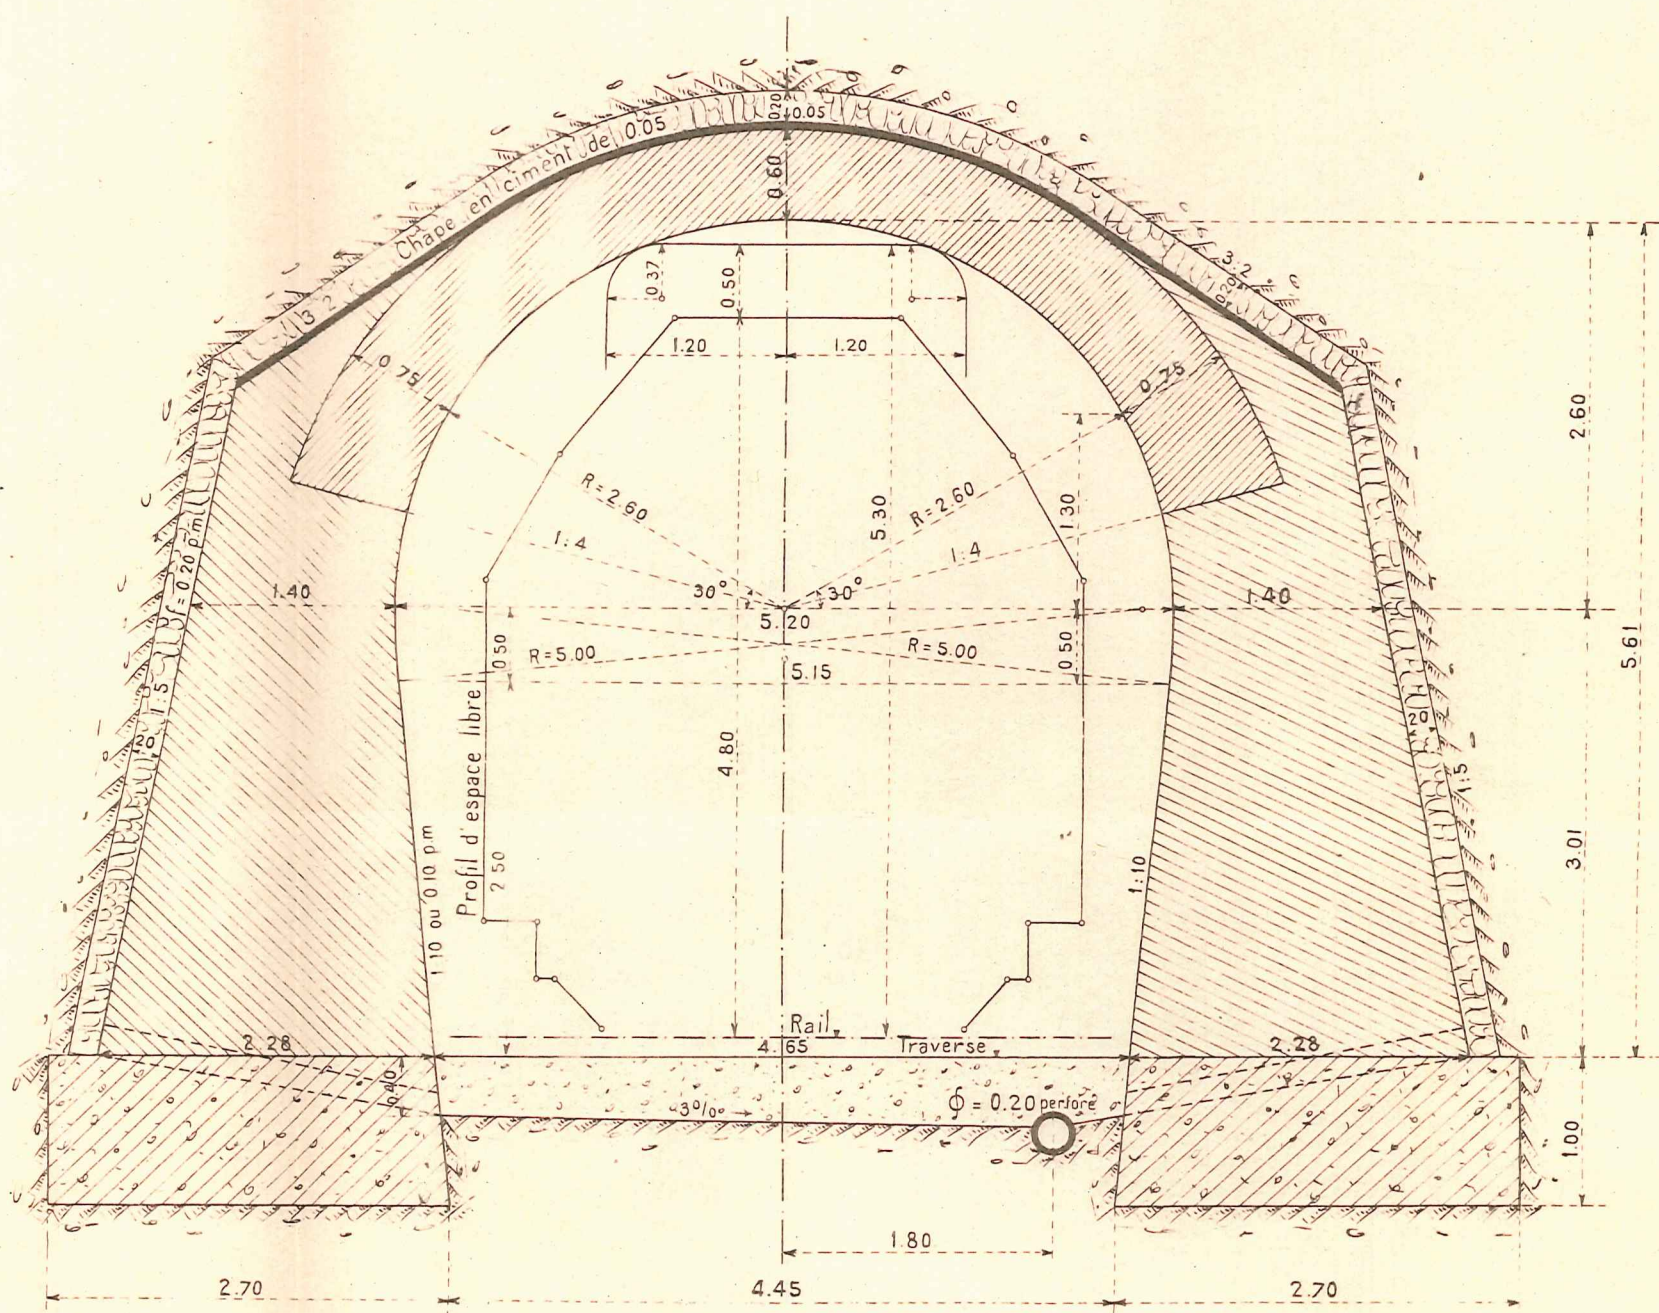

Belon de fondation =	5 ^m 3
Maçonnerie piedsroits =	14 ^m 4
— " — voûte =	5 ^m 4
Blocaçe =	3 ^m 6
Chape en ciment =	8 ^m 3