


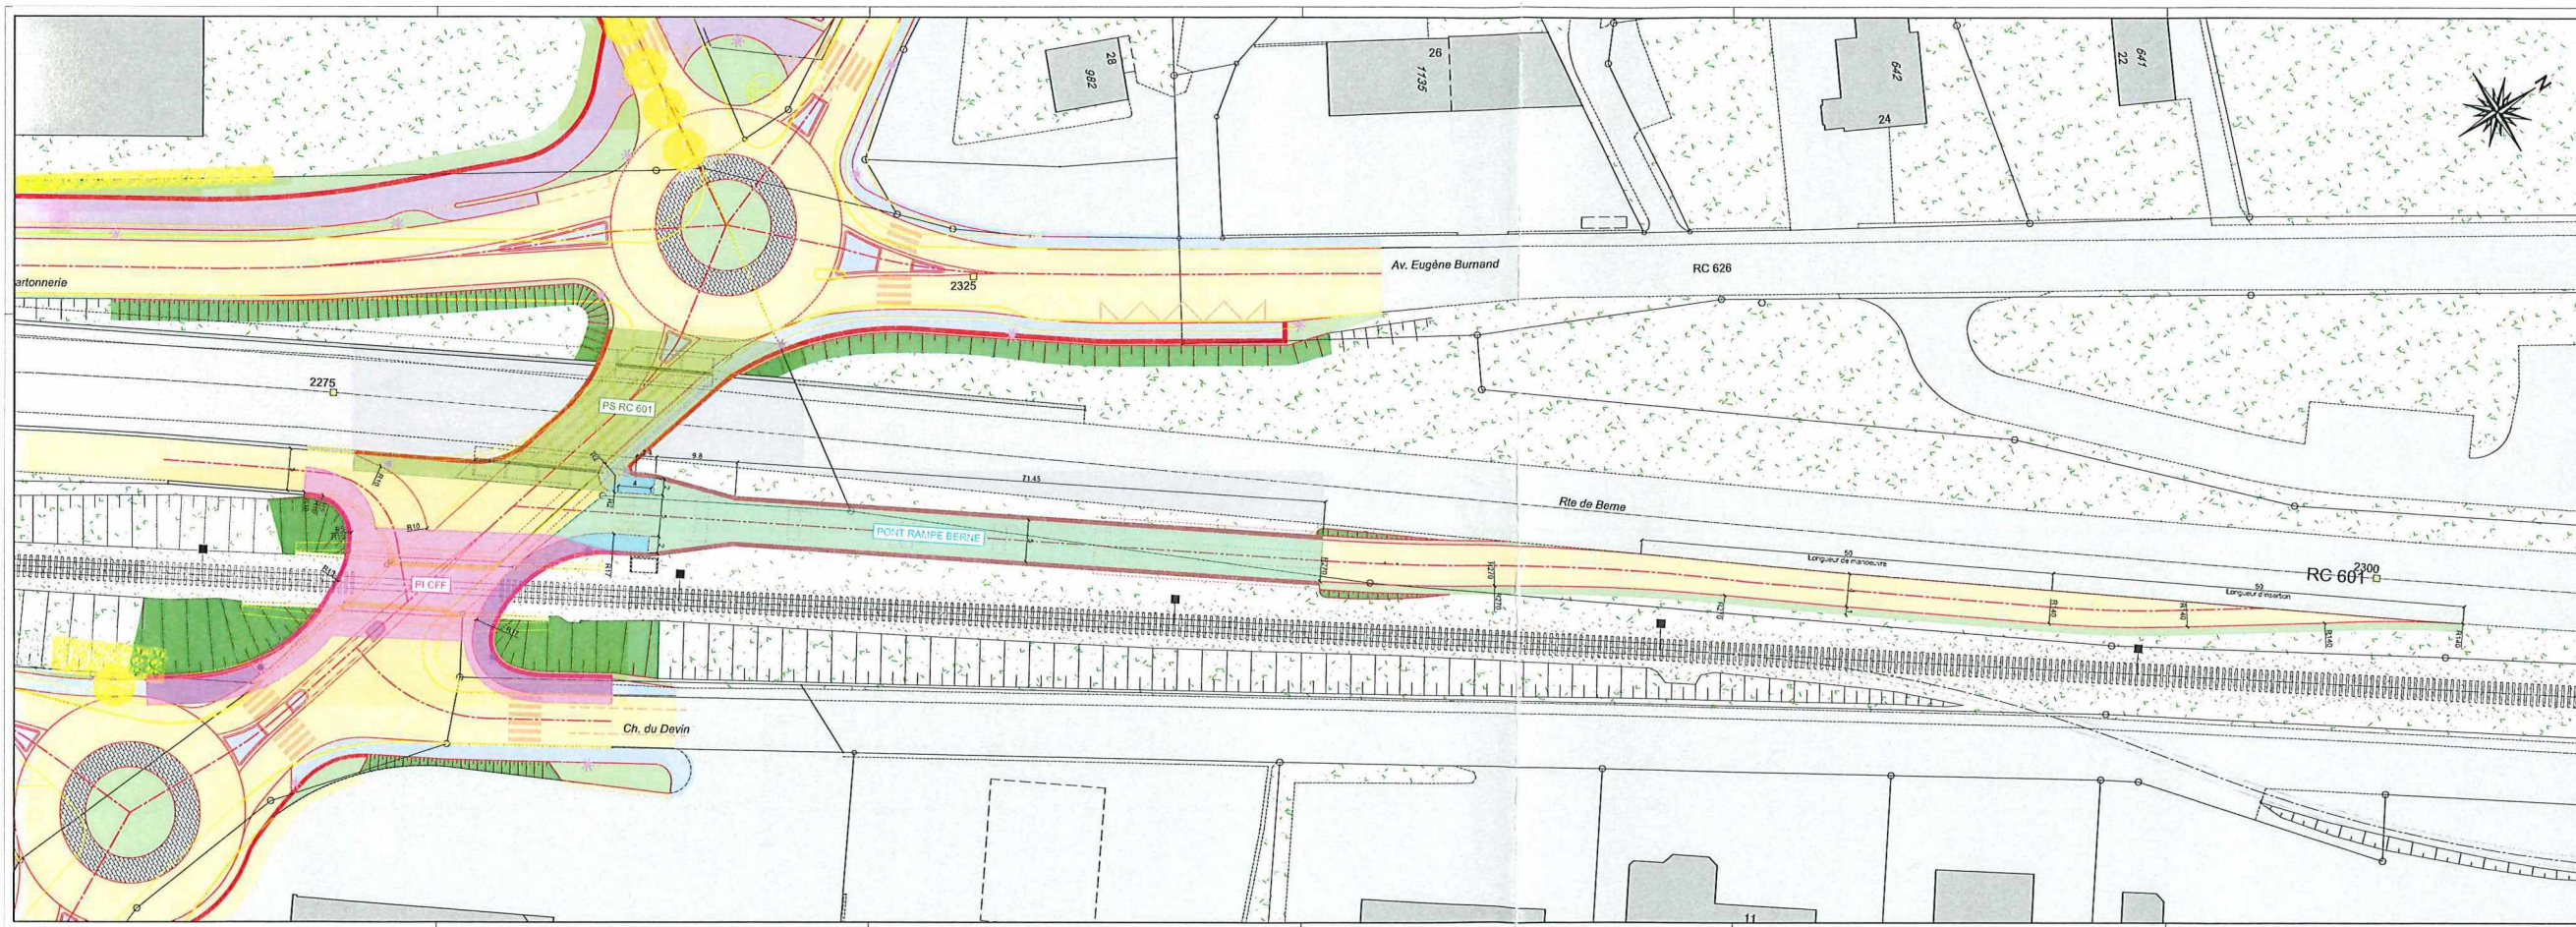

LEGENDE

Chaussée principale		Ouvrage d'art	
Surface carrossable		Pavés gris	
Trottoir		Surface en grave	
Surface verte		Herbe	
Bâtiment		Candélabre	

DÉPARTEMENT DE LA CULTURE, DES INFRASTRUCTURES ET DES RESSOURCES HUMAINES
 DIRECTION GÉNÉRALE DE LA MOBILITÉ ET DES ROUTES
 DIVISION INFRASTRUCTURES

RC 601 Jonction Moudon Sud - Sorbiers
 COMMUNE DE MOUDON

Réaménagement de la jonction Sud
 Zone Ouvrages - Situation générale
SOUSSION - CE4600004765

Dessiné par: King et Associés		JMJ DGR		N° d'affaire: 601.023	Plan: 01 B 701
Inté: 22.03.2024	Date: 04	Des: SM	Contr: SM	Échelle: 1:250	Format: A3
Éléments concernés: Version initiale				Description modification:	

Distribution autorisée par M.O.
☐ Non ☐ Oui Date: _____