



Situation 1:500

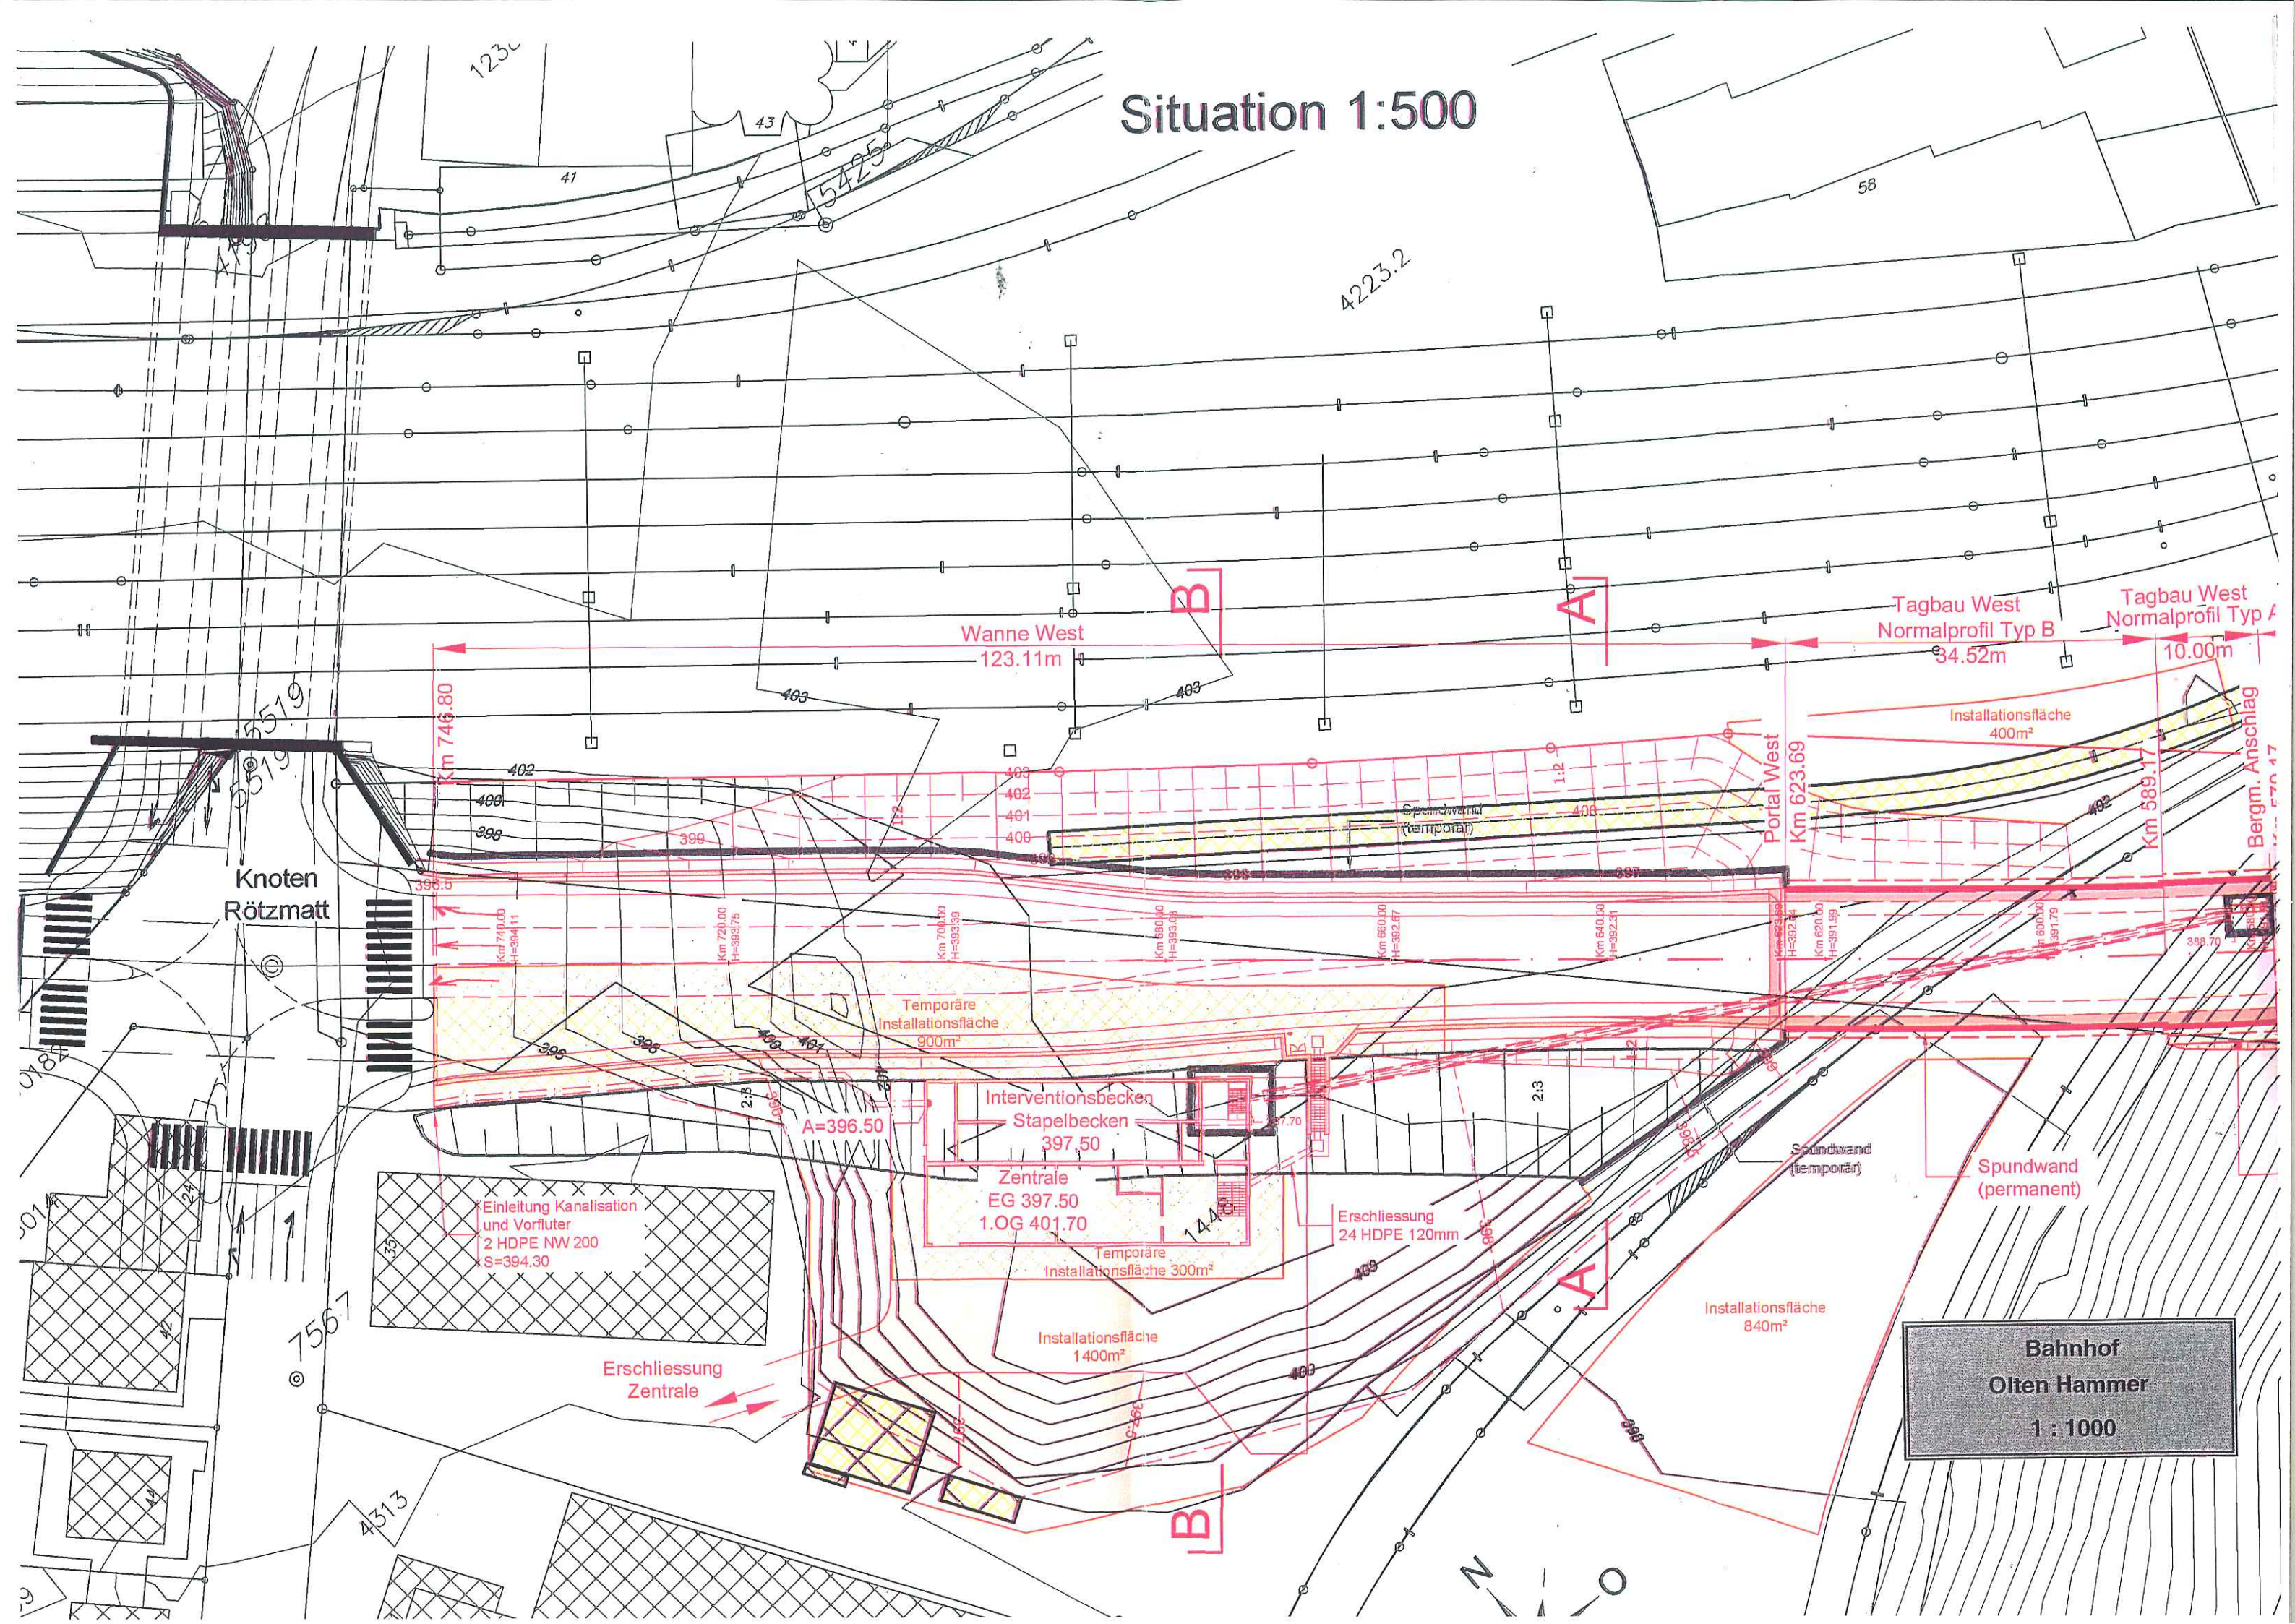

Schnitt B-B, 1:100

Km 0+675.00

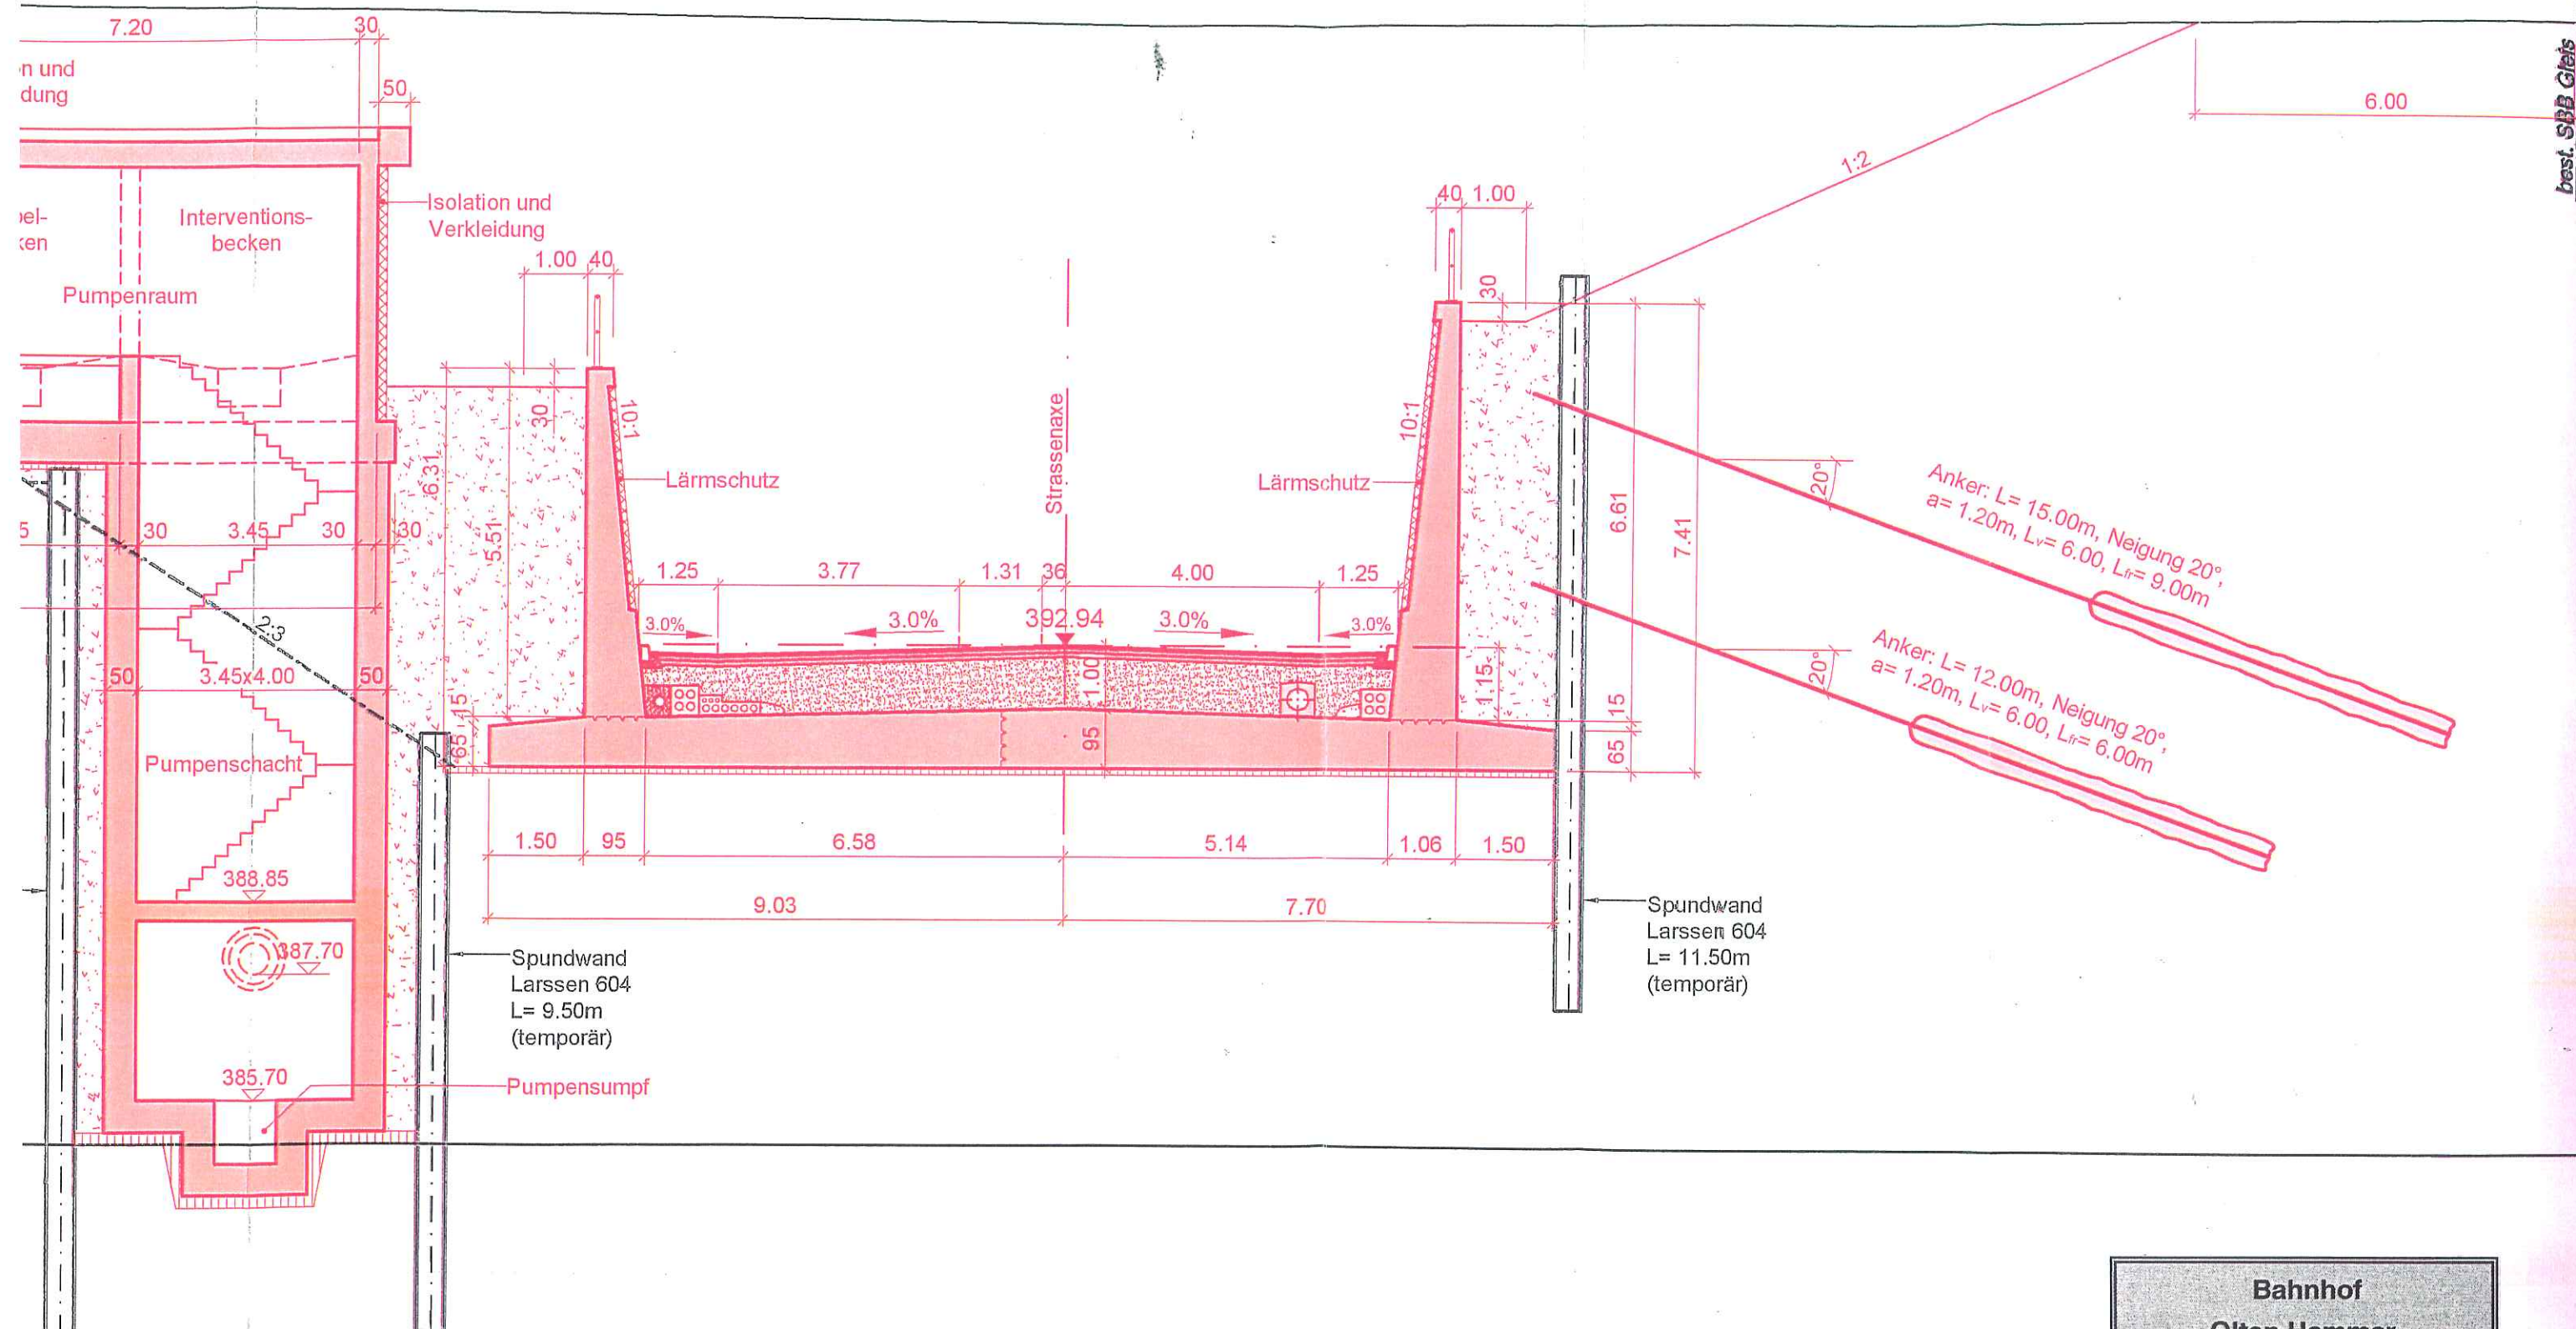

Bahnhof
Olten Hammer
1 : 1000

Betriebszentrale Tunnel Hausmatt

